

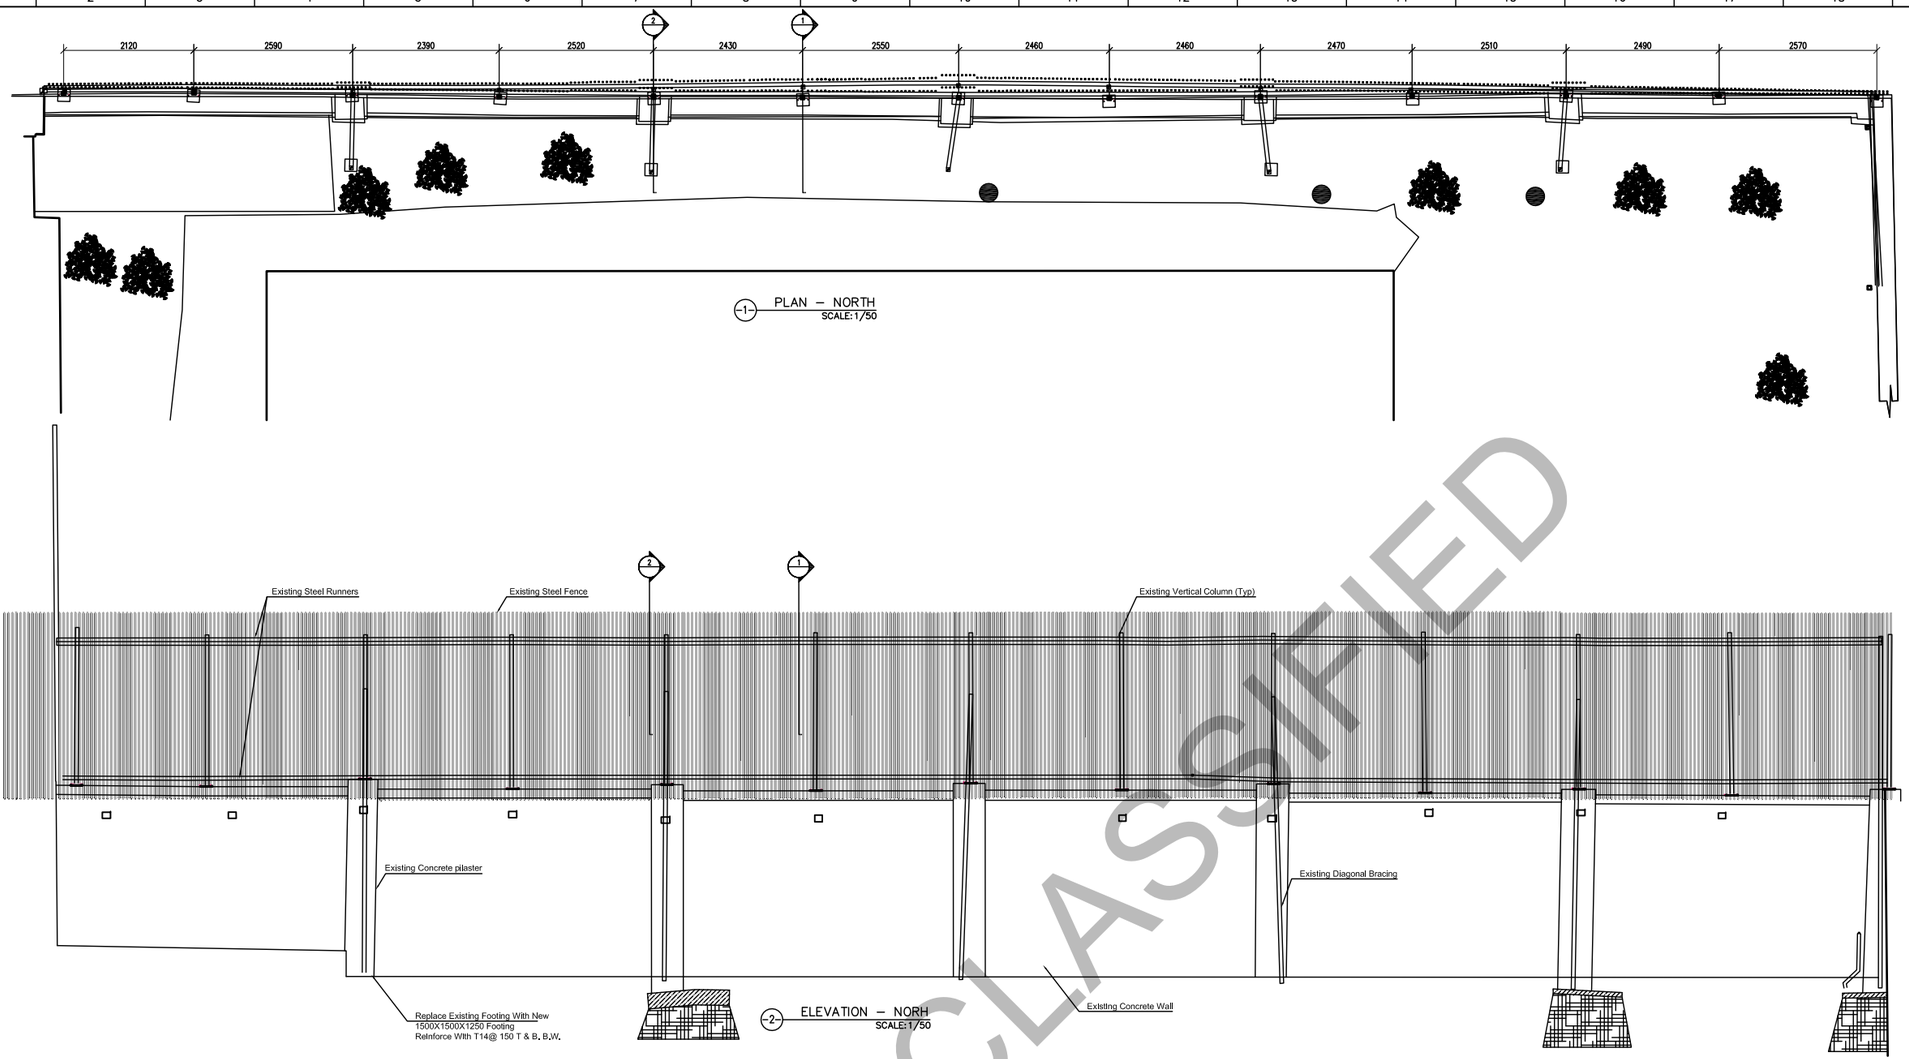


-1- PLAN – NORTH
SCALE:1/50


-2- ELEVATION – NORTH
SCALE:1/50

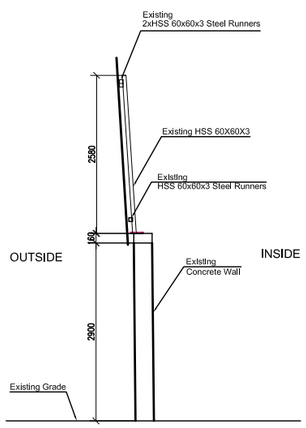

-3- WALL SECTION 1– NORTH
SCALE:1/50

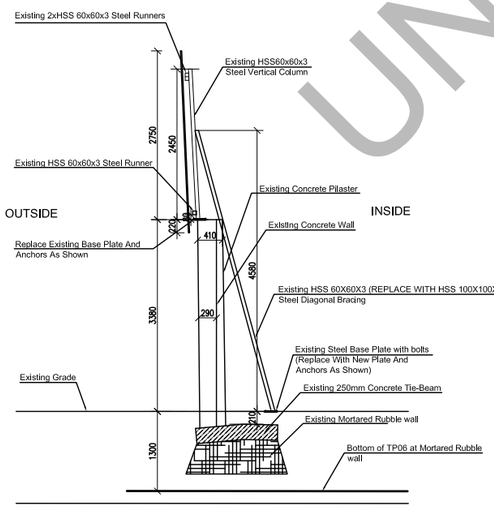

-4- WALL SECTION 2– NORTH
SCALE:1/50

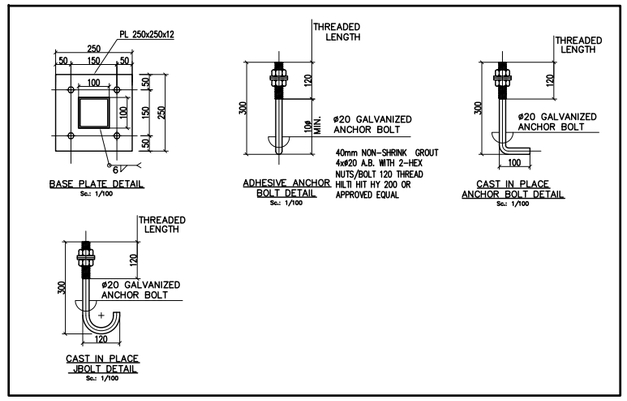

STRUCTURAL DESIGN CRITERIA:

1–	DESIGN CODES	– ASCE – 7 – 05 – UNIFORM BUILDING CODE 1997 EDITION – AISC – LRFD	
2–	DESIGN WIND SPEED IMPORTANCE FACTOR EXPOSURE	45m/s (3Sec GUST) 1.0 C	
3–	SEISMIC	ZONE 3 – UBC 97	Z=0.3
4–	F'c	28 MPa	

STRUCTURAL STEEL NOTES:

1– DUE TO AS BUILT CONDITIONS DIMENSIONS SHOWN MAY NOT MATCH EXISTING DIMENSIONS. THE CONTRACTOR SHALL VERIFY AND COORDINATE ALL EXISTING DIMENSIONS AND ELEVATIONS PRIOR TO FABRICATION OF STEEL AND COMMENCING CONSTRUCTION.

2– REVIEW ALL PROJECT DOCUMENTS PRIOR TO DESIGN. REPORT ANY DISCREPANCIES TO ARCHITECT/ENGINEER PRIOR TO PROCEEDING WITH WORK.

3– COORDINATE STRUCTURAL PLANS WITH OTHER DRAWINGS THAT ARE PART OF THE CONTRACT DOCUMENTS FOR ANCHORED, EMBEDDED OR SUPPORTED ITEMS WHICH MAY AFFECT THE STRUCTURAL STEEL DESIGN.

4– ALL DETAILS AND SECTIONS ON THE DRAWINGS ARE INTENDED TO BE TYPICAL AND SHALL BE CONSTRUED TO APPLY TO ANY SIMILAR SITUATION ELSEWHERE ON THE PROJECT EXCEPT WHERE A SEPARATE DETAIL IS SHOWN.

5– CONTRACTOR SHALL REPORT ANY INTERFERENCE TO ENGINEER FOR REVIEW.

6– FABRICATION AND ERECTION OF STRUCTURAL STEEL SHALL CONFORM TO THE AISC "MANUAL OF STEEL CONSTRUCTION," NINTH EDITION AND THE AISC "SPECIFICATION FOR STRUCTURAL STEEL BUILDINGS," LATEST EDITION.

7– ALL STRUCTURAL AND MISCELLANEOUS STEEL TO CONFORM TO ASTM A36 WITH A MINIMUM YIELD STRENGTH OF 248 MPa.

8– ALL HIGH-STRENGTH BOLTS SHALL MEET THE REQUIREMENTS OF THE "SPECIFICATIONS FOR STRUCTURAL JOINTS USING ASTM A325M OR A490M BOLTS", WITH MINIMUM A HARDENED NUT AND ONE HARDENED WASHER FOR EACH BOLT U.N.O.

9– ALL SHOP AND FIELD WELDING SHALL BE DONE BY CURRENTLY QUALIFIED WELDERS IN ACCORDANCE WITH AWS D1.1 "STRUCTURAL WELDING CODE," LATEST EDITION.

10– USE E70XX LOW HYDROGEN ELECTRODES FOR ALL WELDING UNLESS NOTED OTHERWISE. GRIND SMOOTH ALL EXPOSED WELDS.

11– SUBMIT STRUCTURAL STEEL SHOP DRAWINGS PRIOR TO FABRICATION. CLEARLY SHOW ALL ASSUMPTIONS, REFERENCES, DETAILS, PIECE MARKS AND CONNECTIONS ON ERECTION DRAINGS.

12– NO HOLES ARE ALLOWED IN COLUMNS UNLESS SPECIFICALLY NOTED OR DETAILED ON STRUCTURAL DRAWINGS.

13– SHOP PRIME PAINT ALL STRUCTURAL STEEL WITH ONE COAT TNEMEC 10–99, OR EQUAL.

14– UNLESS NOTED OTHERWISE, ALL BOLTS SHALL BE MINIMUM 20MM DIAMETER ASTM A325M AND SHALL BE BEARING TYPE CONNECTIONS.

15– ALL BOLTS CAST IN CONCRETE SHALL CONFORM TO ASTM A36M OR A307M.

16– TUBE COLUMNS SHALL CONFORM TO ASTM A500, GRADE B, WITH A MINIMUM YIELD STRESS OF 317 MPa.

17– DO NOT WELD TO EMBEDS UNTIL CONCRETE HAS CURED AT LEAST 72 HOURS. USE APPROPRIATE WELDING PROCESSES TO LIMIT HEAT BUILD–UP IN EMBED TO AVOID PLATE EXPANSION AND CRACKING OF CONCRETE.

18– FIELD TIGHTEN HIGH–STRENGTH BOLTS IN ACCORDANCE WITH AISC "SPECIFICATIONS FOR STRUCTURAL JOINTS USING ASTM A325 BOLTS".

UNCLASSIFIED

United States Department of State
OVERSEAS BUILDINGS OPERATIONS
Washington, D.C.

U.S.EMBASSY FENCE

DAMASCUS
SYRIA

WARNING: This document is the property of the U.S. Government. Further reproduction and/or distribution is prohibited without the express written permission of: Overseas Buildings Operations, U.S. Department of State, Washington, DC, 20522–0812. Information on this document is not to be altered except with the written approval of the individual whose seal appears hereon.

Revisions		
R00	100% CONSTRUCTION	JULY 2024

ARCHITECTURAL & ENGINEERING DESIGN FIRM
erga GROUP
naccach. mar mansour str. gebrayel bldg
tel +961 4 524 124 fax +961 4 524 224
70344 antelias - lebanon www.erga.com
dubai abu dhabi fujairah doha manama jeddah riyadh cairo damascus baghdad algeria abuja perth miami

Release For Construction:	
OBO/PE/PM	OBO/PE/EE

Drawing Title
FENCE WALLS
AMBASSADOR'S HOUSE NORTH OF TENNIS YARD

OBO Project Number	DRAWING Scale	Discipline: –	Plot Nbr.: –
4240		Sector: –	Building: –
OBO File Name	OBO Plot Scale	Phase	
4240C–T–101	SHOWN AT	☐CONCEPT ☐SDS ☐DCM ☒CDCE ☐FINAL	

Date	JULY 2024	Sheet Number
Drawn By	GKO	EHU
Checked By	EMO	C -T-101-
Approved By	EMO	
Project Number	4240	
Classification	UNCLASSIFIED	