



**US Army Corps
of Engineers®**



**New Construction and Seismic Upgrades
For White City Veterans Affairs
Southern Oregon Rehabilitation Center and Clinics
Design-Build Request For Proposal for B300 and B301**

**REQUEST FOR PROPOSAL VOLUME 3 - APPENDICES
20 MARCH 2025**

Contract No. W912DY20D0054 /
Task Order No. W9127N24F0032
A/E Project No. 2024-004

VOLUME 3 - APPENDICES**TABLE OF CONTENTS**

- A. Topographic Survey
- B. Supporting Site Plan and Infrastructure Information
- C. Stormwater Facility Design Report
- D. Water, Storm, and Sanitary As-Builts
- E. Detention Pond Maintenance Manual
- G. Fire Flow Test
- H. Geotechnical Report
- I. Memorandum Building Classification
- J. Finishes and Signage Standards
- K. Technology Responsibility Matrix
- L. White City VA EA
- M. Sole Source Items
- P. Architectural Aesthetic
- Q. Owners Project Requirements
- R. Site Photos
- S. Water Report
- T. NFPA 99 Risk Assessment
- U. Hazardous Materials Survey

Topographic Survey

Located at:
Southern Oregon Rehabilitation Center and Clinics, aka V.A. Domiciliary
8495 Highway 62,
Section 17, Township 36 South, Range 1 West, W.M.,
(White City) Jackson County, Oregon

Survey For:
Sherlock, Smith and Adams, Inc.
3047 Carter Hill Road
Montgomery, Alabama, 36111

Survey By:
Pariani Land Surveying
17 South Platt Avenue, Suite C
Eagle Point, OR 97524

Survey Notes:
This topographic surveying project was performed at the request of Sherlock, Smith and Adams, Inc for the purpose of creating an existing conditions site map of the areas within the perimeter roadway. As part of the contractual agreement, spot elevations were omitted and the only feature elevations that were collected are the utilities and the finished floor of the buildings.

The utilities shown on this map is a combination of data collection processes. The One-Call utility locate system (811) was initially utilized throughout the limits of this survey. With many of these utilities being privately owned, not many utilities were marked by this service. A Ground Penetrating Radar (GPR) service was contacted to see if the GPR would identify any of the underground utilities. With the soil type being a mix of loamy, clay, gravels and cobbles, the GPR was not able to penetrate the ground surface more than about 2 feet. We opted to utilize radio detection utility locate equipment to locate the underground utilities. This worked well, particularly, the Line Tracer that inserts into the gravity utilities. In those cases where we were able to insert this Line Tracer, we achieved good results. Also, we utilized the as-built, marked up plans provided to us to aid in identifying some of the pipe sizes and line locations that could not be determined otherwise.

Along the southerly side of 91st Avenue, between Building 210 and Building 214, the storm drainage system has a very strong chemical odor and steam rising from the storm drain manholes. We did not investigate as to the source.

In general, the manholes for the gravity utilities were functioning well and in good shape. However, some of the catch basins were full of debris, as noted in the structure tables.

The One-Call Locate ticket number for this site is 24280881, called in as a Pre-Survey locate.

The tree symbols shown hereon are not drawn to the scale of the actual trunk or drip radius of the tree. They are shown at a reduced scale for clarity.

Building entryway elevations were measured inside the doorway, or at the threshold if door access was not available. Near Building 208, there was some access limitations, as this building is still under construction.

Field survey and mapping was performed between July, 2024 and October, 2024.

Survey Datum:

HORIZONTAL:
Oregon Coordinate Reference System (OCRS)
Grants Pass-Ashland Zone, NAD 83 (2011), Epoch 2010.0

VERTICAL:
NAVD88, (Geoid12B) derived from GPS Static observations over set survey control monuments throughout the project site.

CIVIL LEGEND:

- CURB
- EDGE OF PAVEMENT
- FENCING, HEIGHT & TYPE NOTED
- NATURAL GAS
- POWER - BURIED
- POWER - OVERHEAD
- RETAINING WALL, HEIGHT & MATERIAL NOTED
- PRESSURE SANITARY SEWER, SIZE NOTED
- GRAVITY SANITARY SEWER, SIZE NOTED
- TELEPHONE - BURIED
- TELEPHONE - OVERHEAD
- WATER LINE, SIZE NOTED
- STORM DRAIN LINE, SIZE NOTED

SYMBOLS:

- STORM DRAIN MANHOLE
- CATCH BASIN
- SANITARY SEWER MANHOLE
- POWER/UTILITY POLE
- GUY WIRE
- TELEPHONE/COMMUNICATIONS RISE
- WATER METER
- WATER VALVE
- FIRE HYDRANT
- HOSE BIB/YARD HYDRANT
- IRRIGATION CONTROL VALVE
- SITE LIGHT
- SIGN
- 6"Ø - 12"Ø DECIDUOUS TREE, U.N.O.
- 6"Ø - 12"Ø CONIFER TREE, U.N.O.
- SURVEY CONTROL POINT
- UTILITY CONDUIT
- UNLESS NOTED OTHERWISE

- ASPHALT
- CONCRETE
- GRAVELLED AREA

Sheet 1: Overall Topo
Sheet 2: SW Topo Area
Sheet 3: NW Topo Area
Sheet 4: SE Topo Area
Sheet 5: NE Topo Area/Utility
Sheet 6: Utility Structure Data
Sheet 7: Utility Structure Data

NO.	DESCRIPTION	REV.	BY	CHKD.	BY	DATE
REVISIONS TO DRAWINGS						
This document or any part thereof in detail or design concept is the property of Pariani Land Surveying and shall not be copied in any form without the written authorization of Pariani Land Surveying.						

WARNING
LINE IS 2 INCHES
AT FULL SIZE
(IF NOT 2" SCALE ACCORDINGLY)

Pariani Land Surveying
PHONE: (541) 890-1131 EMAIL: JOHN@PARIANILS.COM

REGISTERED
PROFESSIONAL
LAND SURVEYOR


JOHN R. PARIANI
#51382
Renews: December 31, 2026

361W Section 17
Tax Lot 800

Existing Conditions
Overall Topographic Survey


S.O Rehab Center & Clinic
849 Highway 62
White City, OR 97503

PROJECT NO.	2024-873	SHEET	1 of 7
DATE:	March 17, 2025		
DRAWN BY:	MNB	DRAWING NO.	T-1
REVIEWED BY:	CJP/JRH		
APPROVED BY:	JRP		
HORZ SCALE: 1" = 100'	VERT SCALE:		REV. NO.

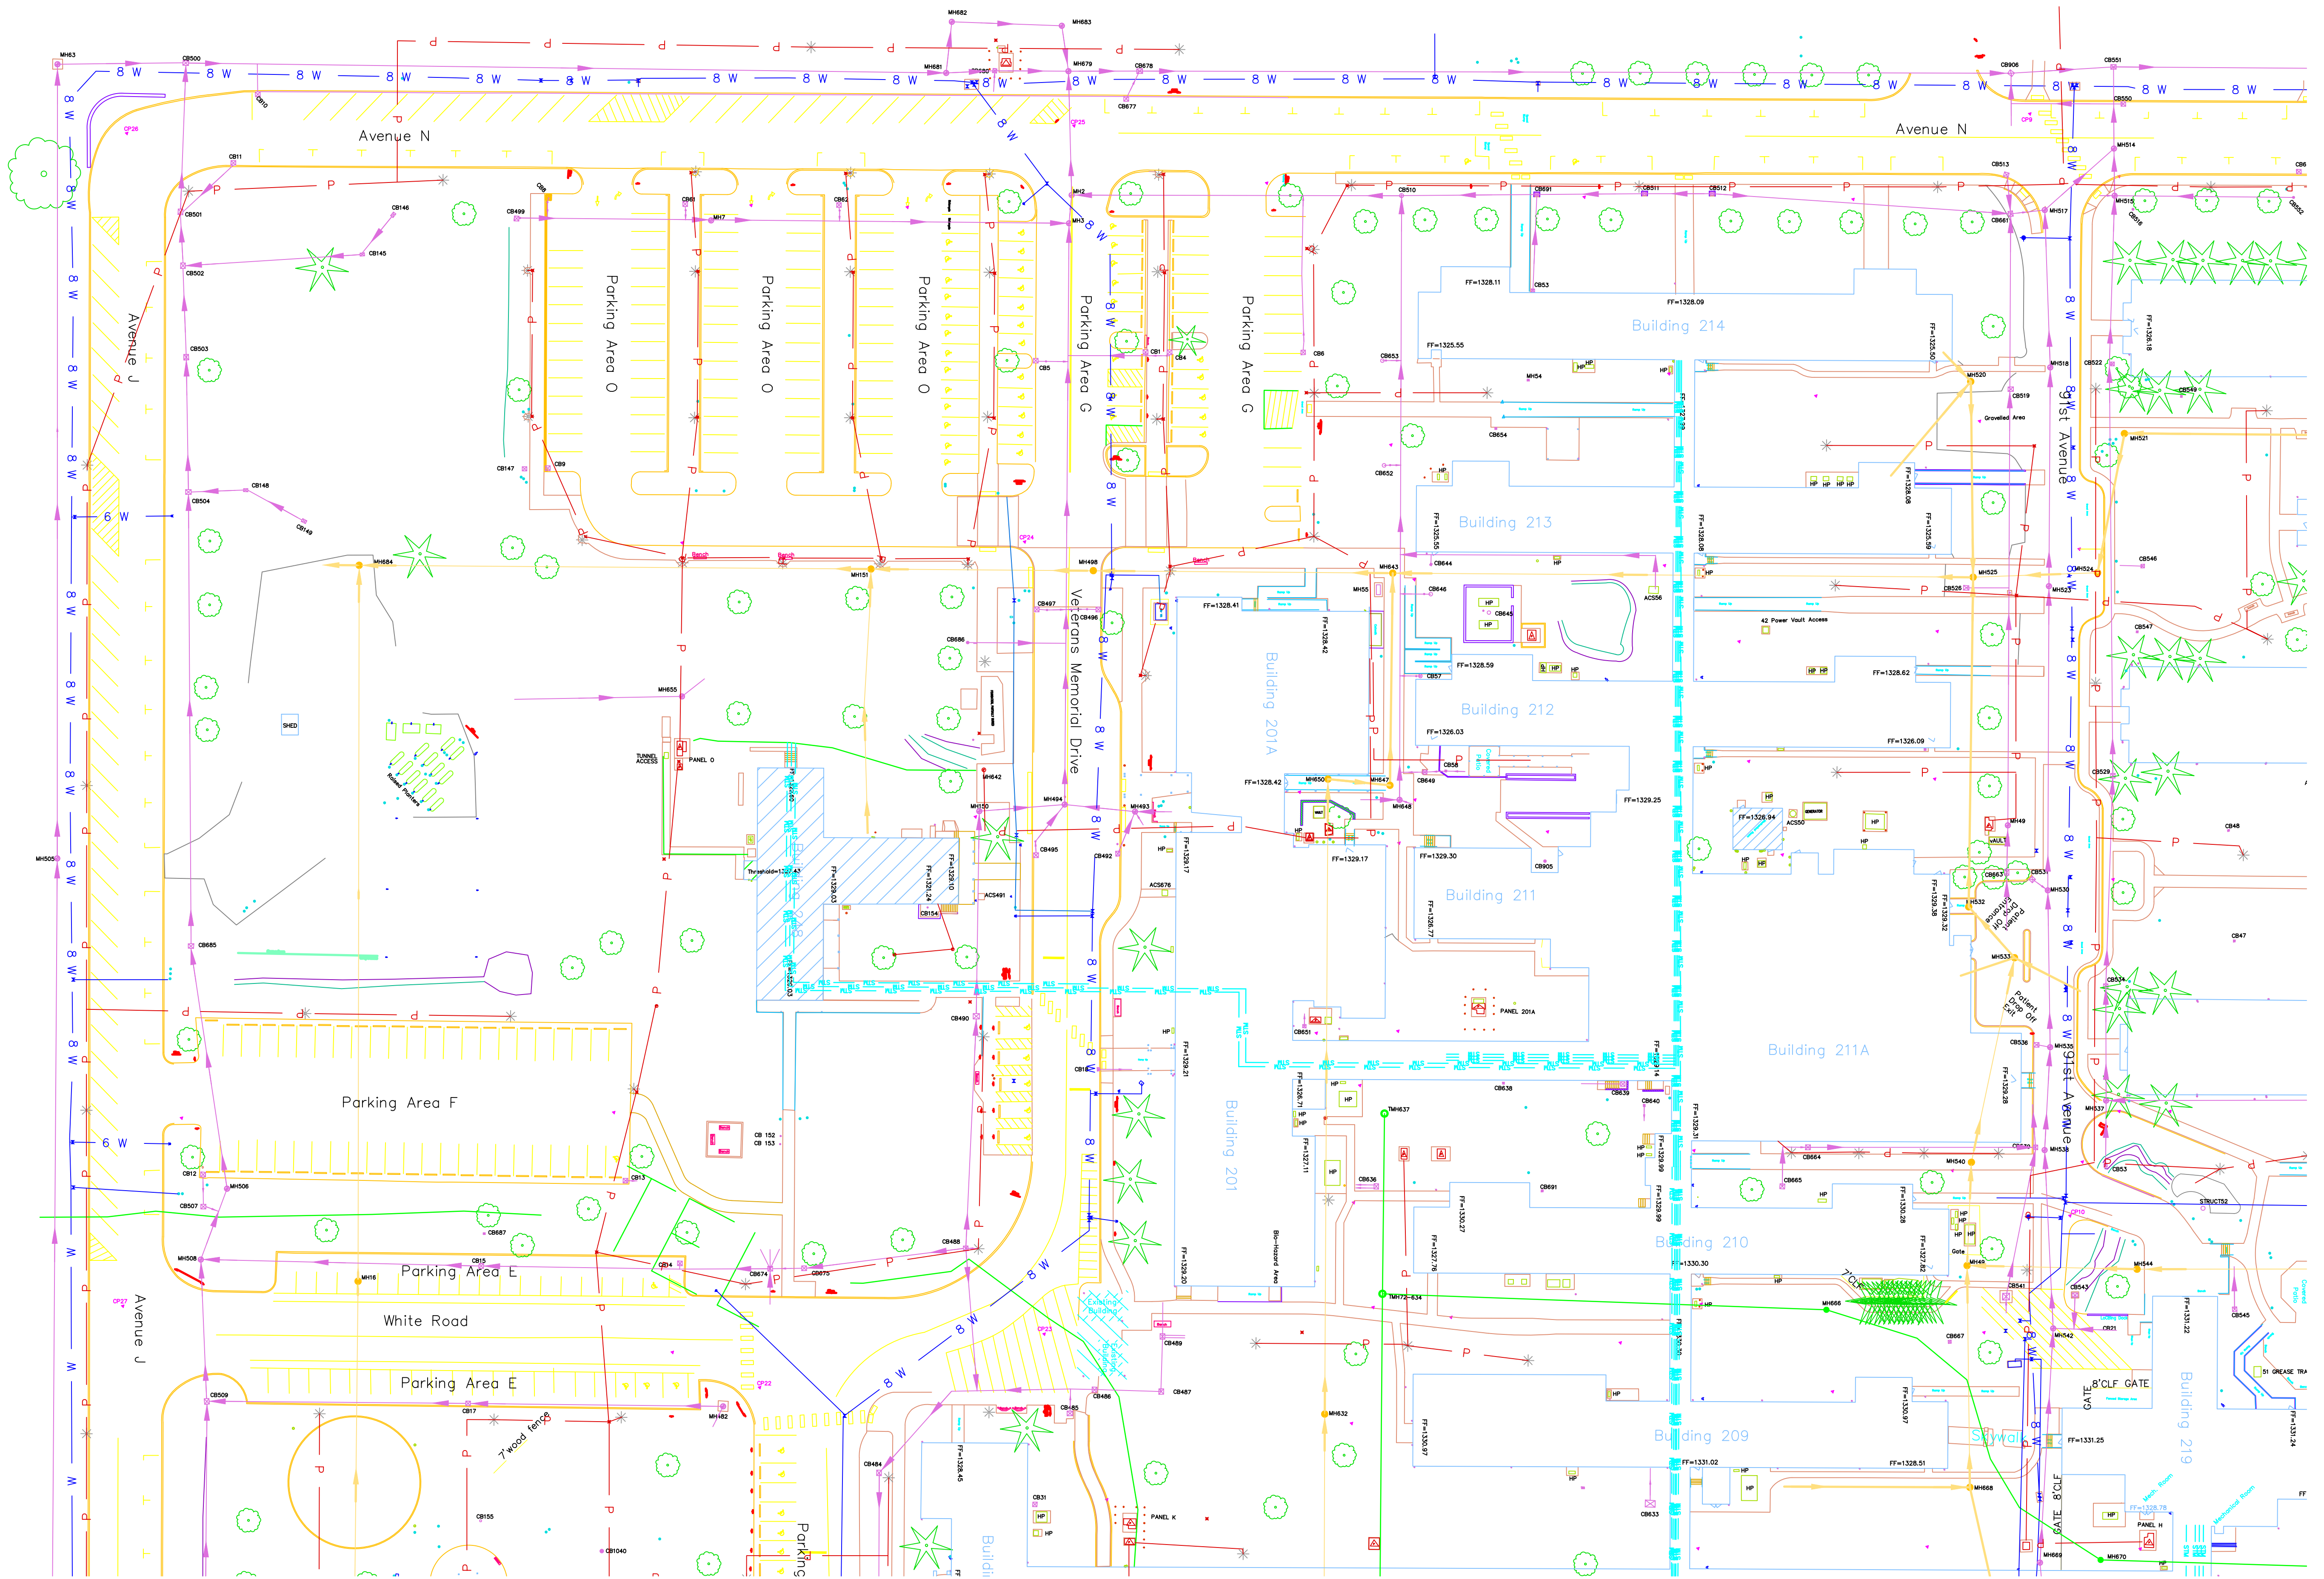

NO.	DESCRIPTION	REV.	BY	CHKD.	DATE
REVISIONS TO DRAWINGS					
This document or any part thereof in detail or design concept is the property of Pariani Land Surveying and shall not be copied in any form without the written authorization of Pariani Land Surveying.					

WARNING
LINE IS 2 INCHES
AT FULL SIZE
(IF NOT 2" SCALE ACCORDINGLY)

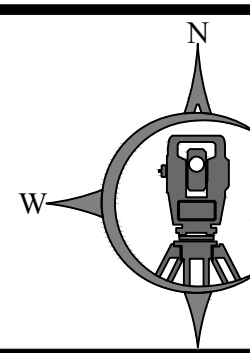


Pariani Land Surveying
PHONE (541) 890-1131 EMAIL: JOHN@PARIANILS.COM



361W Section 17
Tax Lot 800
**Existing Conditions
Topographic Survey**


PROJECT NO. 2024-873		SHEET 2 of 7	
DATE: March 17, 2025		DRAWING NO. T-1	
DRAWN BY: MNB		REV. NO.	
REVIEWED BY: CJP/JRH			
APPROVED BY: JRP			
HORIZ. SCALE: 1" = 40'		VERT. SCALE:	


S.O. Rehab Center & Clinic
8495 Highway 62
White City, OR 97503

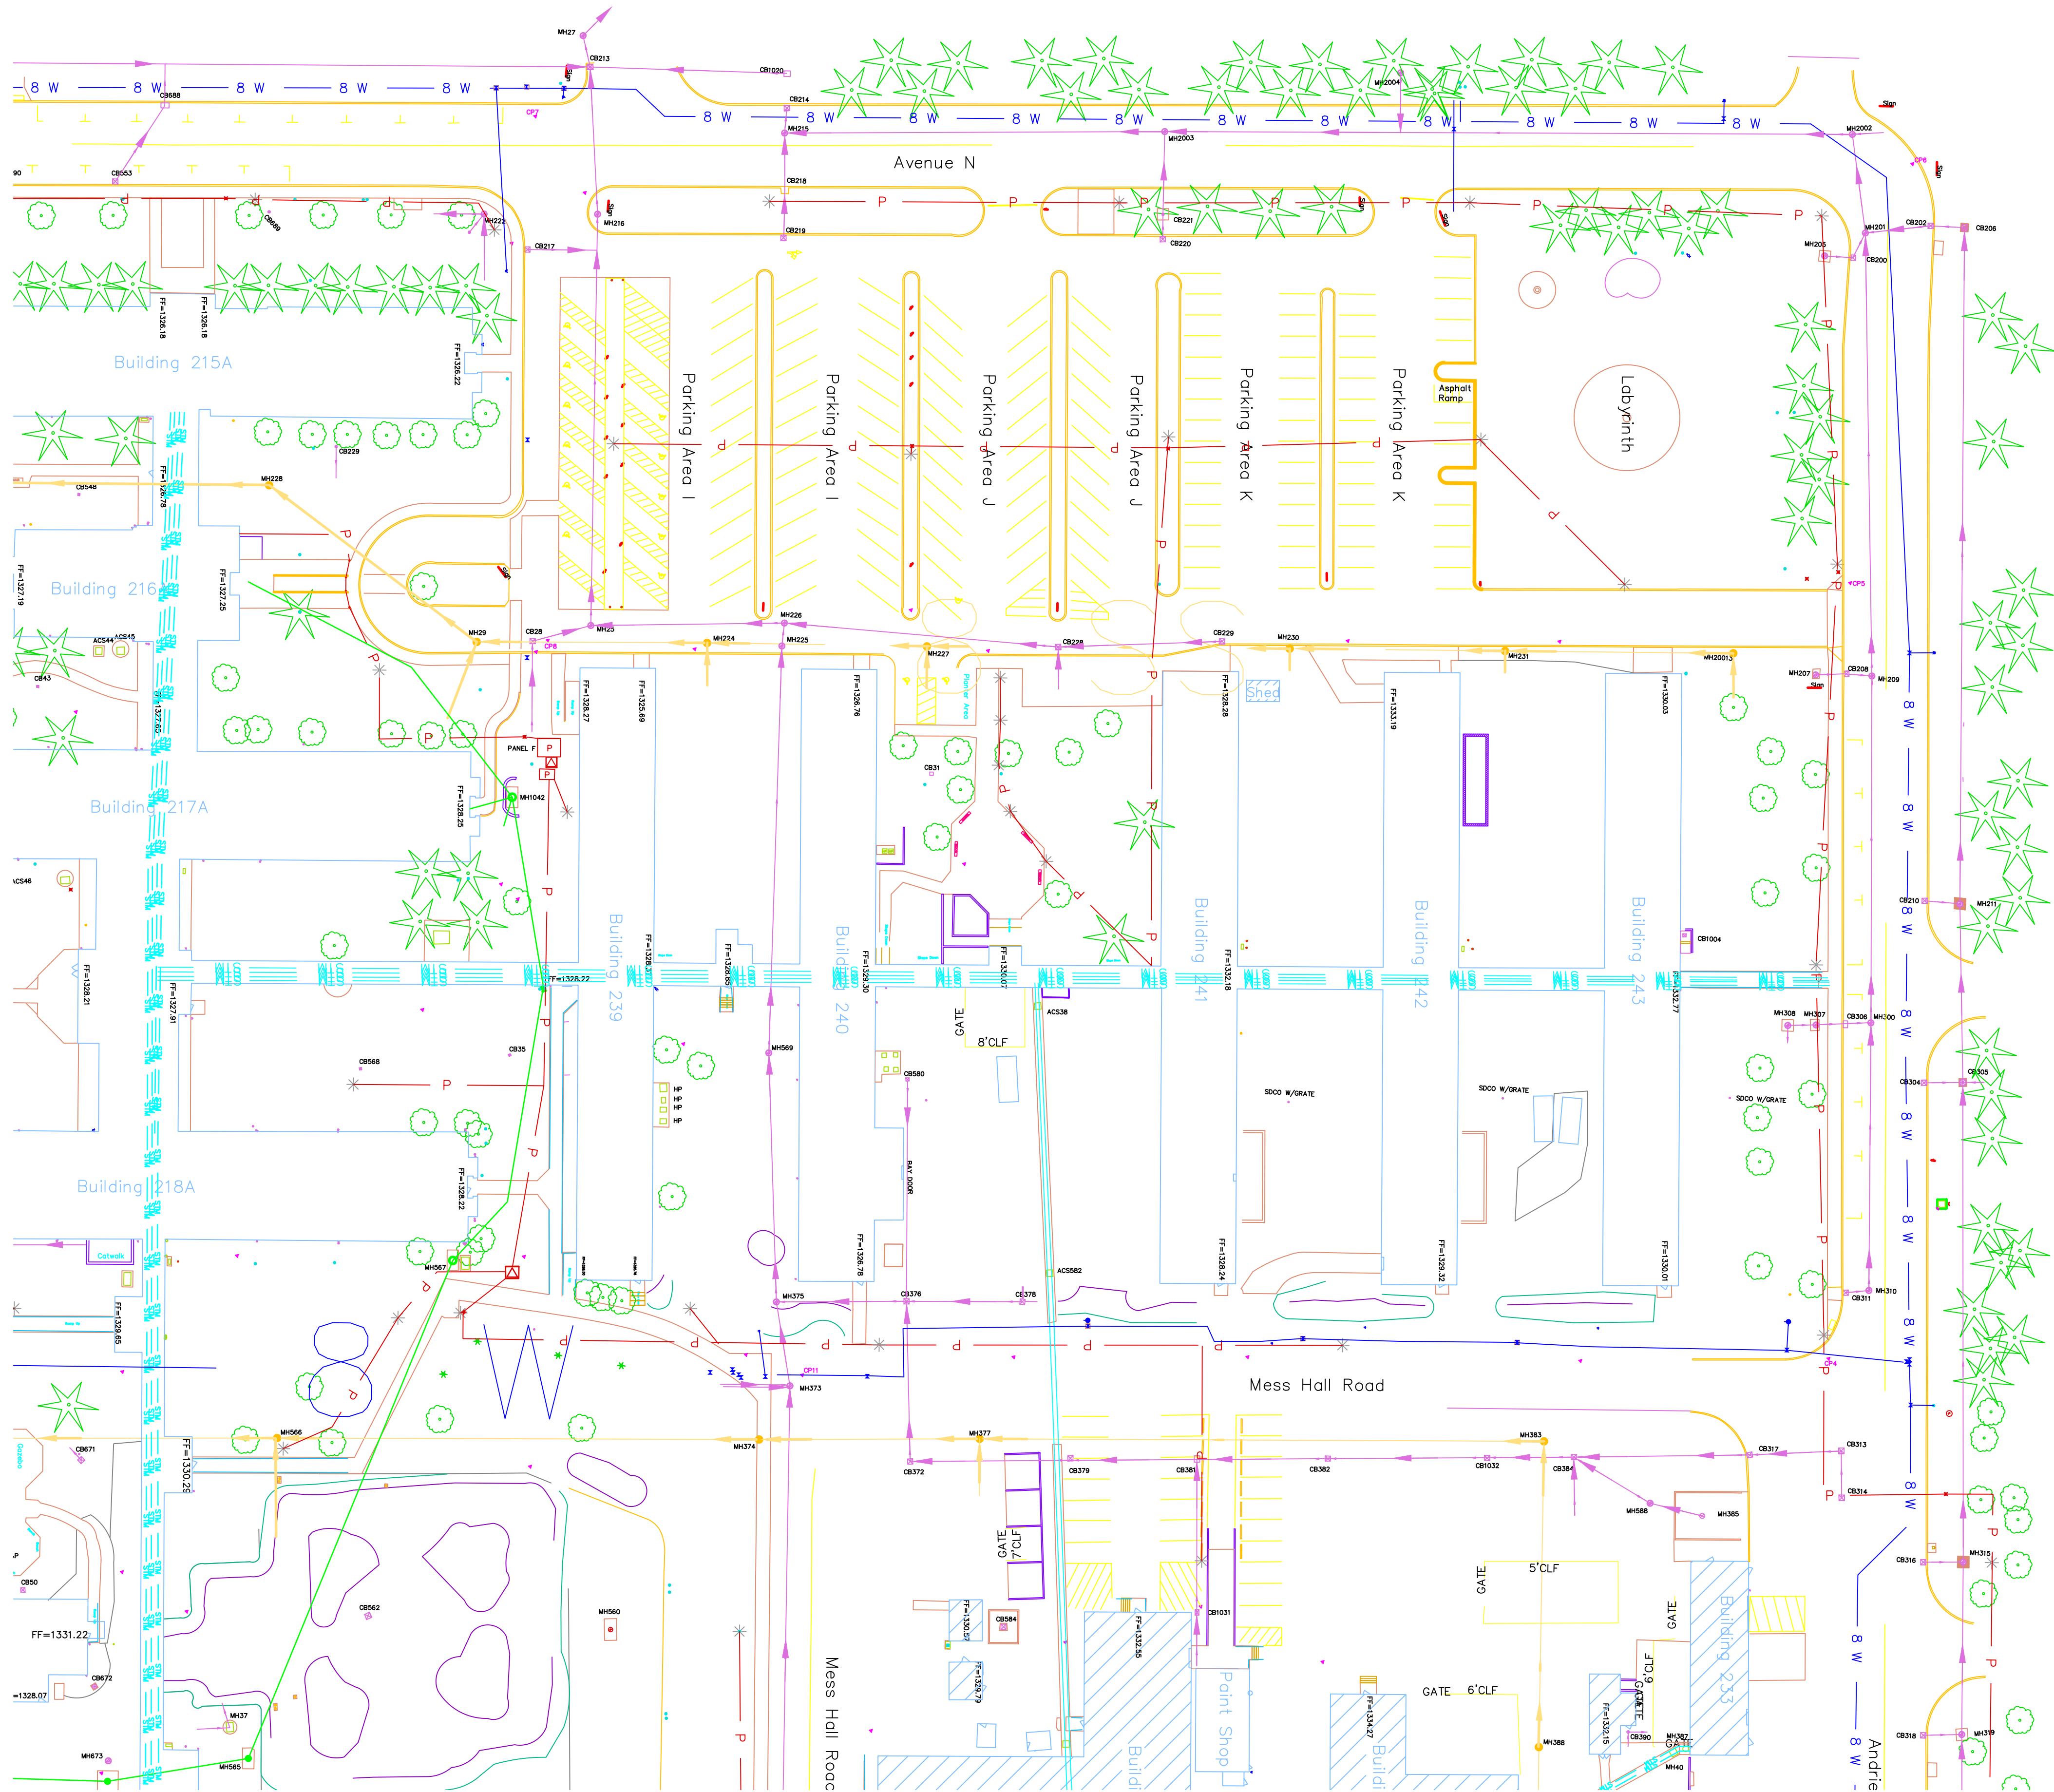

NO.	DESCRIPTION	REV. BY	CHKD. BY	DATE
REVISIONS TO DRAWINGS				
This document or any part thereof in detail or design concept is the property of Pariani Land Surveying and shall not be copied in any form without the written authorization of Pariani Land Surveying.				

WARNING
LINE IS 2 INCHES
AT FULL SIZE
(IF NOT 2" SCALE ACCORDINGLY)

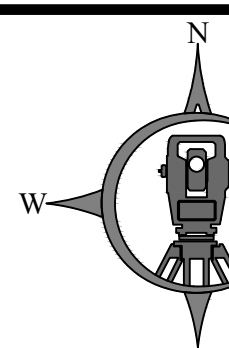 **Pariani Land Surveying**
PHONE: (541) 890-1131 EMAIL: JOHN@PARIANILS.COM

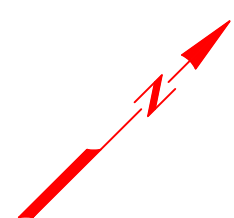

REGISTERED
PROFESSIONAL
LAND SURVEYOR


JOHN R. PARIANI
#51382
Renews: December 31, 2026

361W Section 17
Tax Lot 800


Existing Conditions
Topographic Survey



S.O Rehab Center & Clinic
8495 Highway 62
White City, OR 97503

PROJECT NO.	2024-873	SHEET	3 of 7
DATE:	March 17, 2025	DRAWN BY:	MNB
REVIEWED BY:	CJP/JRH	APPROVED BY:	JRP
HORZ SCALE: 1" = 40'	VERT SCALE:	DRAWING NO.	T-1
		REV. NO.	

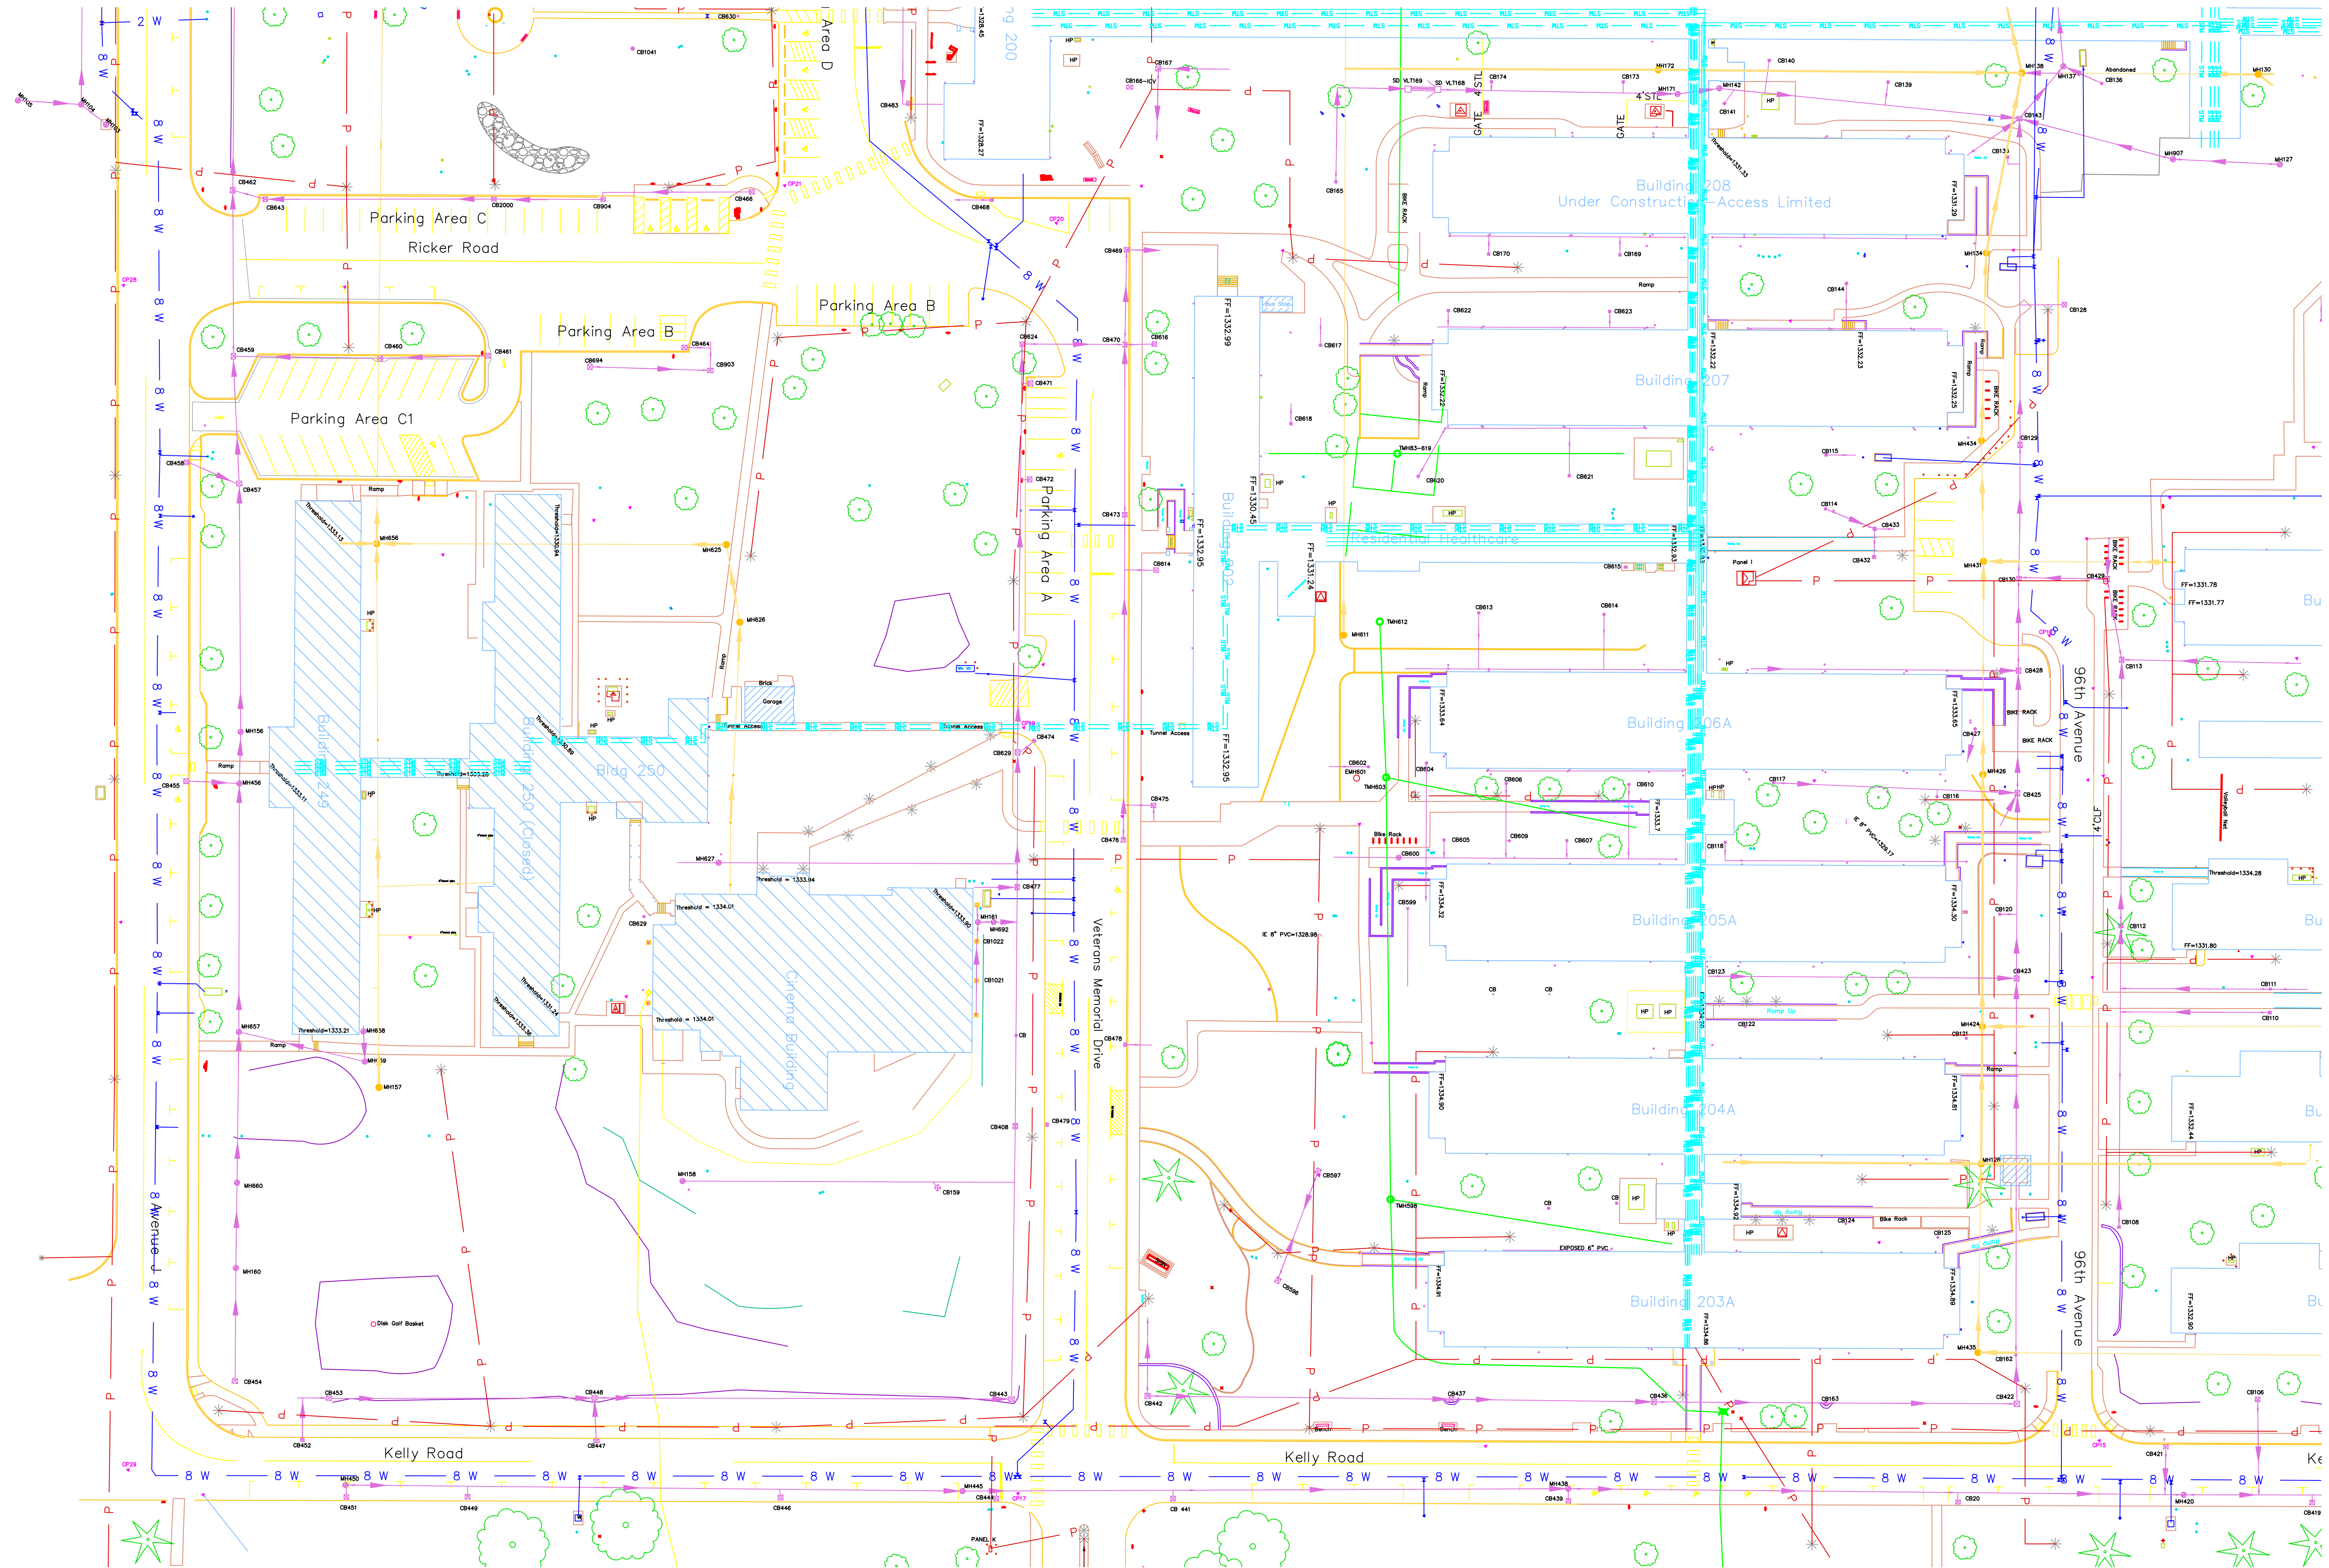

WARNING
LINE IS 2 INCHES
AT FULL SIZE
(IF NOT 2" SCALE ACCORDINGLY)

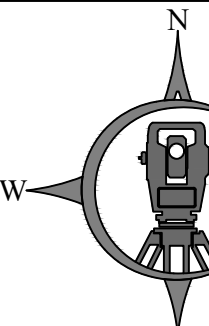**Pariani Land Surveying**
PHONE: (541) 890-1131 EMAIL: JOHN@PARIANILS.COM

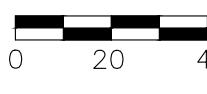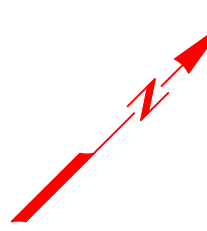

REGISTERED PROFESSIONAL LAND SURVEYOR


JOHN R. PARIANI
#51392
Renews: December 31, 2026

361W Section 17
Tax Lot 800

**Existing Conditions
Topographic Survey**

S.O Rehab Center & Clinic
8495 Highway 62
White City, OR 97503


PROJECT NO.	2024-873	SHEET	4 of 7
DATE:	March 17, 2025	DRAWING NO.	T-1
DRAWN BY:	MNB	REV. NO.	
REVIEWED BY:	CJP/JRH		
APPROVED BY:	JRP		
HORIZ. SCALE: 1" = 40'	VERT. SCALE:		

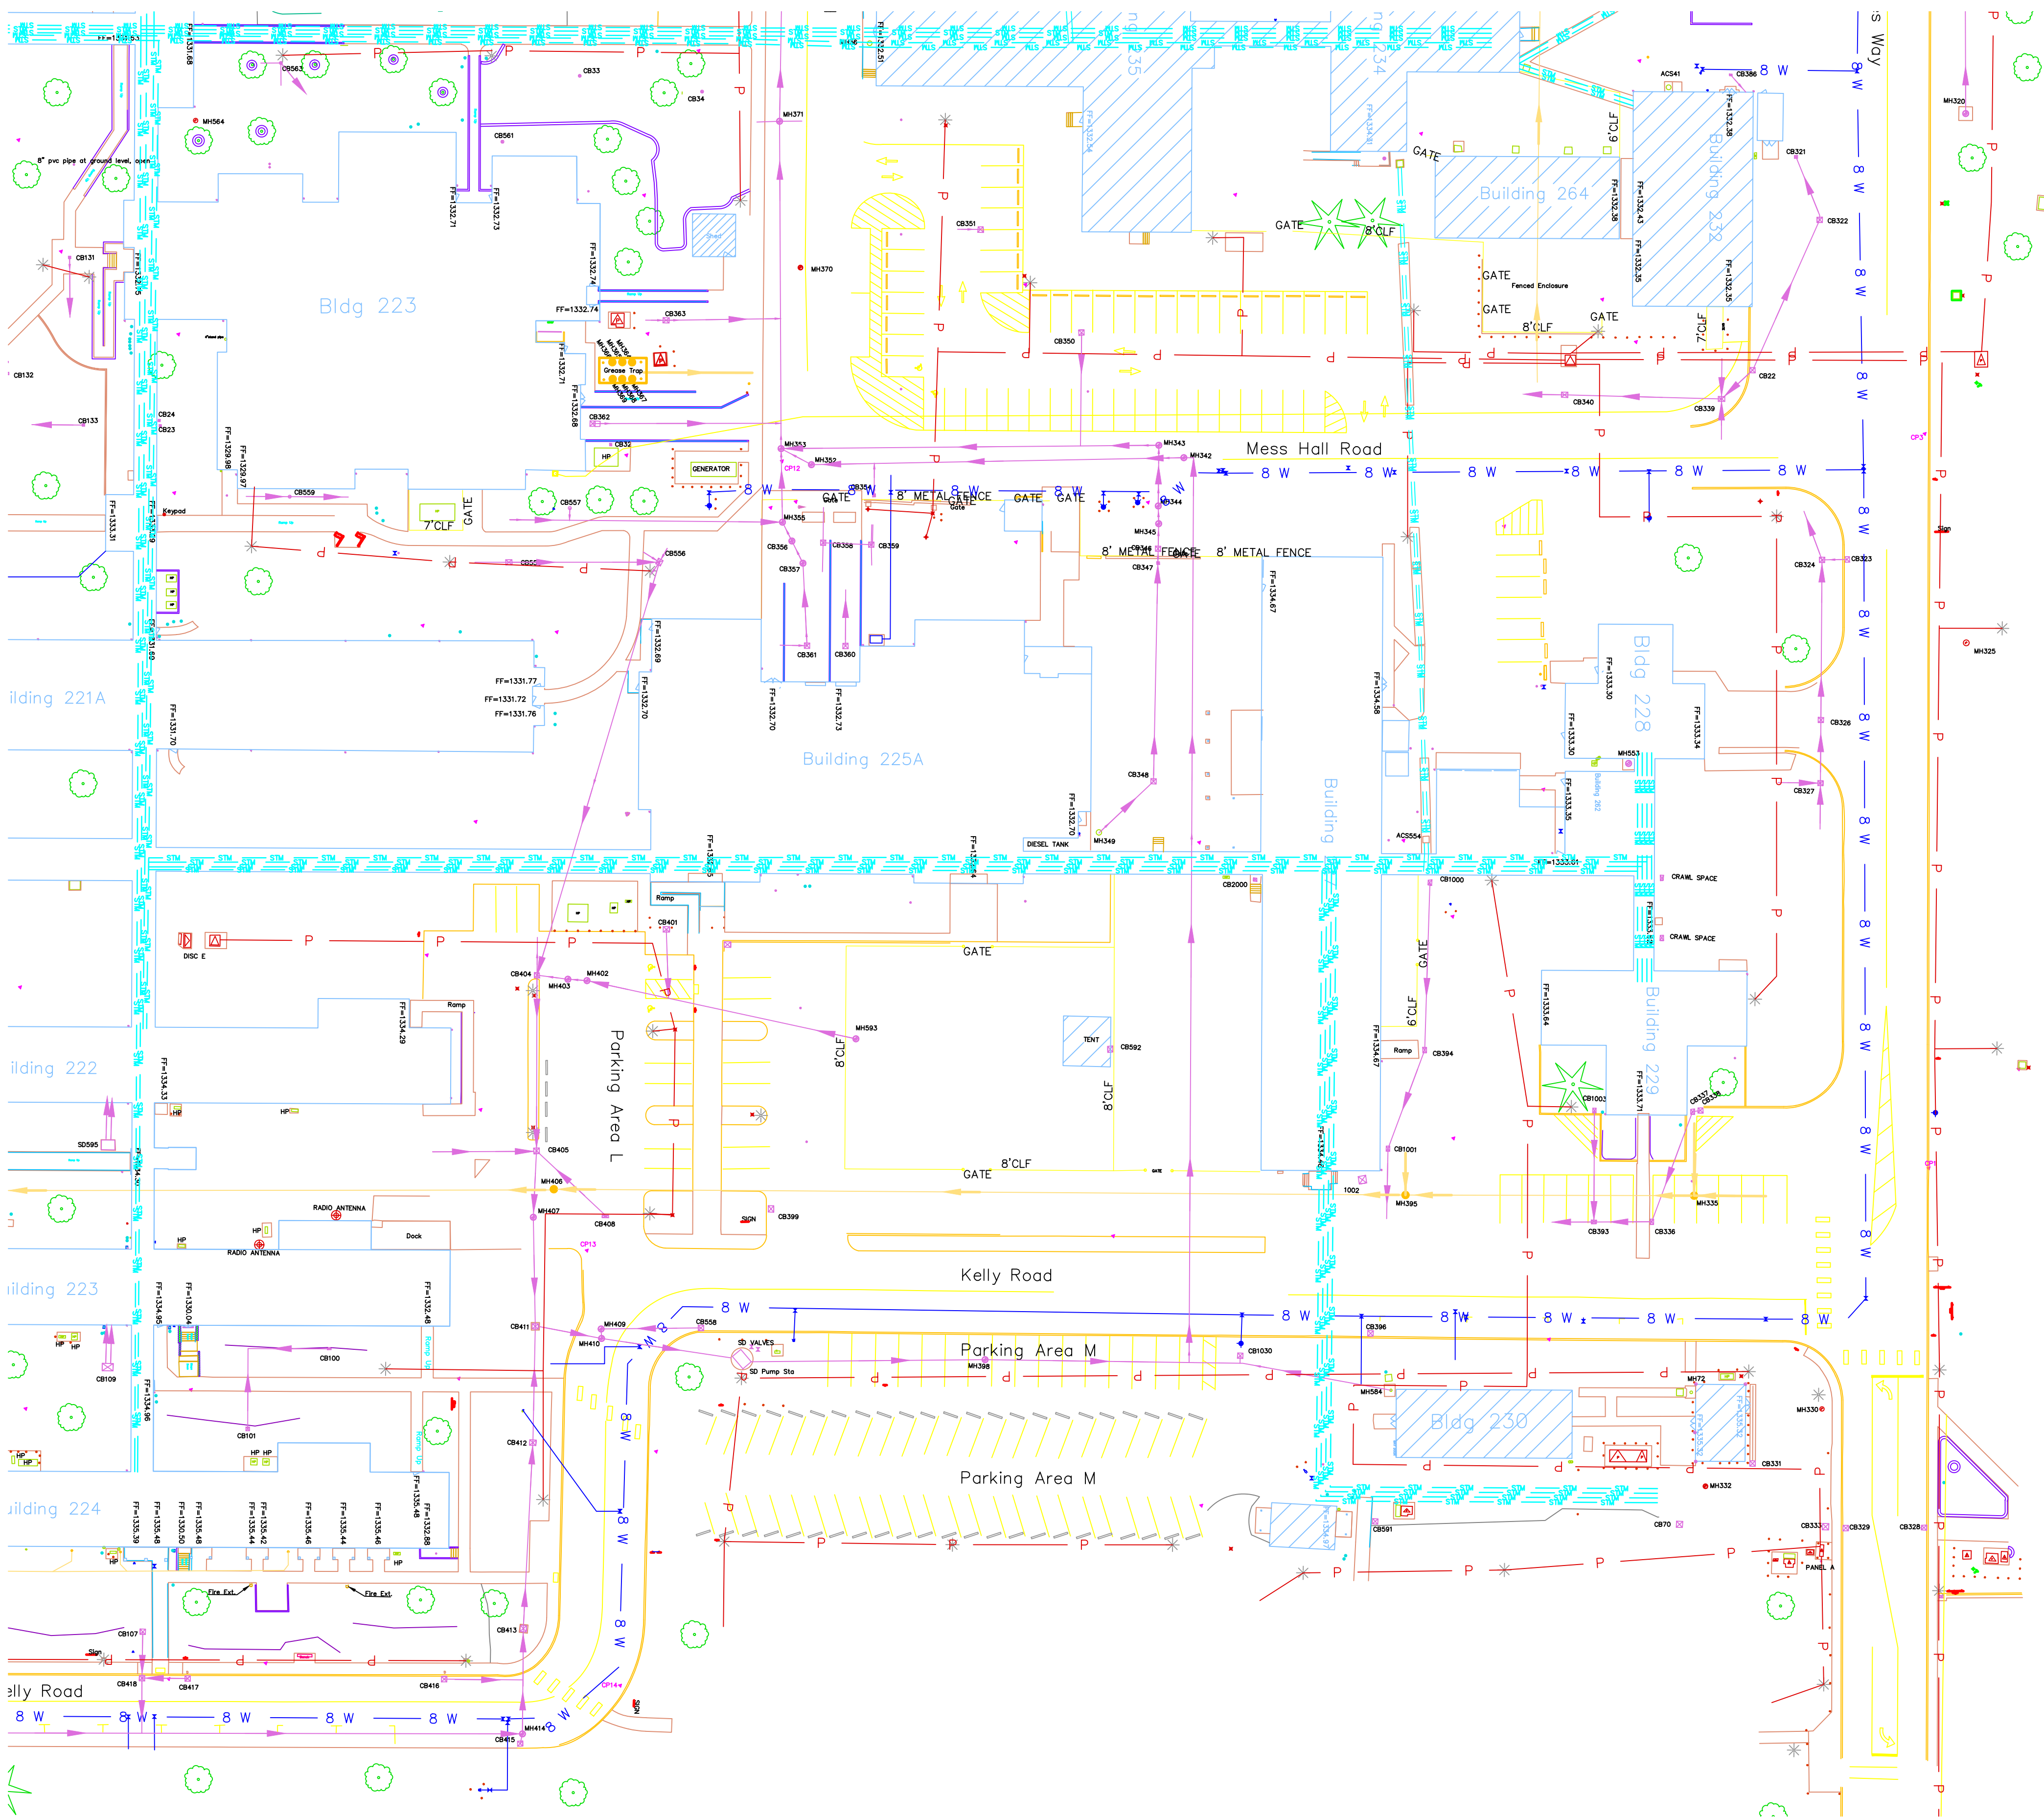



STORM DRAIN STRUCTURES												
0.4	STRUCTURE	Rim Elev	1st invert	1st pipe size/type	2nd invert	2nd pipe size	3rd invert	3rd pipe size/type	4th invert	4th pipe size	5th invert	5th pipe size/type
1	Catch Basin	1325.08	1323.28	8" PVC	1321.48	SUMP						
4	Catch Basin	1324.84	1323.14	8" PVC	1321.24	SUMP						
5	Catch Basin	1325.60	1323.80	8" PVC	1321.95	SUMP						
6	Catch Basin	1324.35	1322.65	8" PVC	1320.65	SUMP						
8	Catch Basin	1325.25	1323.60	8" PVC	1321.55	SUMP						
9	Catch Basin	1325.23	1324.33	WATER LEVEL								
10	Catch Basin	1325.15	1322.25	6" PVC	1321.15	SUMP						
11	Catch Basin	1325.16	1323.86	8" PVC	1320.76	SUMP						
12	Catch Basin	1327.10	1324.60	8" N12	1323.10	SUMP						
13	Catch Basin	1327.21	1327.21		1327.21							
14	Catch Basin	1326.68	1325.13	4" PVC	1325.08	8" PVC	1322.38	SUMP				
15	Catch Basin	1327.12	1327.12	No Access								
17	Catch Basin	1326.98	1325.03	6" PVC	1324.93	10" PVC	1322.88	SUMP				
18	Catch Basin	1327.16	1326.61	3" PVC	1325.16	SUMP						
19	Catch Basin	1334.93		Full of Debris								
20	Catch Basin	1334.64	1331.74	8" PVC	1330.14	SUMP						
22	Catch Basin	1331.82	1329.92	6" PVC	1329.82	8" PVC	1327.52	SUMP		1331.82		
23	Catch Basin			Full of Debris								
24	Catch Basin			BOLTED SHUT								
26	Catch Basin		-5.40	12" PVC	-8.30	24" PVC	-10.05	36" N12	36" N12	-10.10		
28	Catch Basin	1324.50	1322.60	8" PVC	1322.50	12" PVC	1320.90	Sump				
31	Catch Basin	1327.55	1324.95	WW under grate								
33	Catch Basin	1328.89		No Access								
34	Catch Basin	1329.33		No Access								
35	Catch Basin	1325.79		BOLTED SHUT	1325.79							
36	Catch Basin	1332.46		No Access								
43	Catch Basin	1325.94		No Access								
47	Catch Basin	1326.54		No Access	1326.54		1326.54					
48	Catch Basin	1326.20		No Access	1326.20		1326.20					
50	Catch Basin	1328.06	1327.06	SUMP-NO PIPES								
53	Catch Basin	1327.53	1327.03	3" ABS								
57	Catch Basin	1325.29	1324.19	8" PVC	1323.39	SUMP						
58	Catch Basin	1326.46	1325.71	3" ABS	1325.71	3" ABS						
61	Catch Basin	1325.08	1323.38	8" STEEL	1321.38	SUMP						
62	Catch Basin	1325.10	1325.10		1325.10		1325.10			1325.10		
70	Catch Basin	1334.44	1332.99	12" CMP	1332.94	12" CMP	1333.04	2" PVC				
100	Catch Basin	1332.30	N/A	8" CONC	1332.30							
101	Catch Basin	1332.38	1331.73	3" PVC		Full of Water						
106	Catch Basin	1331.73	1330.18	8" PVC	1327.43	SUMP						
107	Catch Basin	1332.16	1330.01	8" PVC	1327.66	SUMP						
108	Catch Basin	1330.94	N/A	full of debris								
109	Catch Basin	1332.30	1329.55	6" CONC								
110	Catch Basin	1330.93	1330.03	Top of Pipe		Full of Debris						
111	Catch Basin	1330.74	1329.94	3" PVC	1329.84	3" PVC						
112	Catch Basin	1330.10	1328.80	8" CONC								
113	Catch Basin	1329.95	1327.75	8" N12	1327.70	8" N12	1327.70	8" N12	SUMP	1325.45		
114	Catch Basin	1329.10		full of debris								
115	Catch Basin	1328.81	1328.16	4" PVC	1327.11	SUMP						
116	Catch Basin	1330.31		full of debris								
117	Catch Basin	1330.62	1329.72	6" PVC								
118	Catch Basin	1331.32	1330.42	6" PVC								
120	Catch Basin	1330.86	1329.96	6" PVC								
121	Catch Basin	1330.90		Full of Debris								
122	Catch Basin	1331.16	1330.36	6" PVC								
123	Catch Basin	1331.97		Full of Debris								
124	Catch Basin	1331.49		Full of Debris								
128	Catch Basin	1329.40	1329.40	No Access								
129	Catch Basin	1329.05	1327.85	6" PVC								
130	Catch Basin	1329.85	1327.65	12" PVC	1327.65	12" PVC	1327.50	12" PVC	SUMP	1326.85		
131	Catch Basin	1329.14	1328.14	6" PVC Oil Sep.								
132	Catch Basin	1329.25	1328.35	Oil Separator								
133	Catch Basin	1329.60	1328.60	Oil Separator								
135	Catch Basin	1328.42	1327.62	4" PVC Oil Sep.	1326.82	SUMP						
136	Catch Basin	1327.79	1326.99	4" PVC	1326.19	SUMP						
139	Catch Basin	1327.88	1327.13	4" PVC Oil Sep.	1326.28	SUMP						
140	Catch Basin	1328.19		No Access								
141	Catch Basin	1328.40	1327.70	4" PVC Oil Sep.	1326.80	SUMP						
143	Catch Basin	1328.61	1325.81	8" PVC	1325.36	12" PVC	1323.11	18" PVC	12" PVC	1323.06	1322.96	18" PVC
144	Catch Basin	1328.06	1327.41	4" PVC	1326.41	SUMP						
145	Catch Basin	1324.19	1322.24	8" PVC	1322.09	8" PVC						
146	Catch Basin	1323.90	1322.45	8" PVC								
147	Catch Basin	1325.08		No Access								
148	Catch Basin	1324.55	1323.15	4" PVC	1322.95	8" PVC						
148	Catch Basin	1324.62	1323.22	4" PVC	1323.02	8" PVC						
149	Catch Basin	1324.84	1323.84	4" PVC	1324.84							
152	Catch Basin	1326.32		No Access								
153	Catch Basin	1326.28		No Access								
154	Catch Basin	1320.61		No Access			1320.61					
155	Catch Basin	1327.94		full of debris								
158	Catch Basin	1330.30	1326.55	30" N12	1326.10	SUMP						
159	Catch Basin	1332.40	1330.40	6" PVC	1328.00	SUMP						
162	Catch Basin	1331.86	1330.61	10" CONC	1330.61	10" CONC						
163	Catch Basin	1331.66	1330.66	10" CONC	1330.61	10" CONC						
165	Catch Basin	1328.24	1327.59	4" PVC	1326.59	SUMP						
166	Catch Basin	1327.95		No Access								
167	Catch Basin	1327.99	1325.99	8" PVC	1325.69	8" PVC	1325.49	SUMP				
169	Catch Basin	1328.54	1327.79	4" PVC	1326.89	SUMP						
170	Catch Basin	1328.54	1327.79	4" PVC	1326.89	SUMP						
173	Catch Basin	1327.31	1326.66	4" PVC	1325.66	SUMP						
174	Catch Basin	1327.30	1326.65	4" PVC	1325.65	SUMP						
200	Catch Basin	1329.48	1325.98	10" PVC	1325.88	10" PVC	1325.18	SUMP				
202	Catch Basin	1330.28	1325.88	12" PVC	1325.68	12" PVC	1324.68	SUMP				
206	Catch Basin	1329.10	1325.95	12" PVC	1325.90	12" PVC						
208	Catch Basin	1330.48	1327.78	10" PVC	1327.58	12" PVC	1326.58	SUMP				
210	Catch Basin	1331.05	1329.20	8" PVC	1326.75	SUMP						
213	Catch Basin	1324.27	1314.27	36" N12	1314.17	36" N12						
214	Catch Basin	1325.19	1320.89	12" PVC	1320.79	12" PVC	1319.54	SUMP				
217	Catch Basin	1324.42	1319.57	6" PVC	1318.17	SUMP						
218	Catch Basin	1325.26	1321.91	10" PVC	1321.81	12" PVC	1320.16	SUMP				
219	Catch Basin	1325.25	1322.70	10" PVC	1320.85	SUMP						
220	Catch Basin	1326.71	1323.46	10" PVC	1322.41	SUMP						
221	Catch Basin	1326.52	1323.37	10" PVC	1323.27	10" PVC ELBC	1322.02	SUMP				
228	Catch Basin	1326.92	1324.87	8" PVC	1323.42	12" PVC	1323.12	12" PVC	Sump	1323.02		
229	Catch Basin	1327.64		No Access								

NO.	DESCRIPTION	REV.	BY	CHKD.	DATE
REVISIONS TO DRAWINGS					
This document or any part thereof in detail or design concept is the property of Pariani Land Surveying and shall not be copied in any form without the written authorization of Pariani Land Surveying.					

WARNING
LINE IS 2 INCHES
AT FULL SIZE
(IF NOT 2" SCALE ACCORDINGLY)

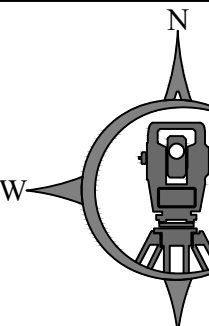

Pariani Land Surveying
PHONE: (541) 890-1131 EMAIL: JOHN@PARIANILS.COM

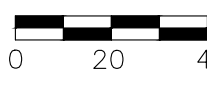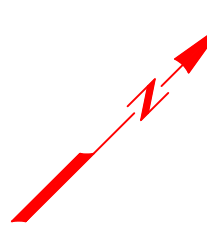

REGISTERED
PROFESSIONAL
LAND SURVEYOR

JOHN R. PARIANI
#51352
Renews: December 31, 2026

361W Section 17
Tax Lot 800

**Existing Conditions
Topographic Survey**

S.O Rehab Center & Clinic
8495 Highway 62
White City, OR 97503

PROJECT NO. **2024-873**

DATE: **March 17, 2025**

DRAWN BY: **MNB**

REVIEWED BY: **CJP/JRH**

APPROVED BY: **JRP**

HORZ SCALE: 1" = 40' VERT SCALE:

SHEET **5 of 7**

DRAWING NO. **T-1**

REV. NO.

STORM DRAIN STRUCTURES

0.4	STRUCTURE	Rim Elev	1st invert	1st pipe size/type	2nd invert	2nd pipe size/type	3rd invert	3rd pipe size/type	4th invert	4th pipe size	5th invert	5th pipe size/type
229	Catch Basin	1327.64		No Access								
229	Catch Basin	1324.80	1324.00	6" PVC	1324.80							
304	Catch Basin	1331.15	1329.75	8" PVC	1326.75	SUMP						
305	Catch Basin	1330.86	1327.86	8" PVC	1327.81	8" PVC	1327.76	10" PVC	12" PVC	1327.76		
306	Catch Basin	1331.05	1327.85	8" PVC	1327.95	8" PVC	1326.15	SUMP				
306	Catch Basin	1331.05	1327.95	8" PVC	1327.85	8" PVC	1326.15	SUMP				
311	Catch Basin	1331.43	1329.73	8" PVC	1327.13	SUMP						
313	Catch Basin	1331.36	1329.76	6" PVC	1329.71	6" PVC	1327.06	SUMP				
314	Catch Basin	1331.36	1329.96	6" PVC	1327.06	SUMP						
316	Catch Basin	1331.70	1329.25	6" PVC	1327.60	SUMP						
317	Catch Basin	1331.50	1329.35	6" PVC	1329.25	6" PVC	1327.20	SUMP				
318	Catch Basin	1331.97	1330.37	8" PVC	1327.97	SUMP						
321	Catch Basin	1332.09		FULL OF DEBRIS								
322	Catch Basin	1332.11	1330.16	6" PVC	1329.86	8" PVC	1327.81	SUMP				
323	Catch Basin	1333.25	1331.75	6" PVC	1328.95	Sump						
324	Catch Basin	1332.96	1331.76	4" Corrugated	1331.51	6" PVC	1331.43	8" PVC	8" PVC	1331.39	1328.96	Sump
326	Catch Basin	1333.05	1331.85	8" PVC	1331.85	8" PVC	1328.65	SUMP				
327	Catch Basin	1333.27	1332.17	4" Corrugated	1332.12	6" PVC	1332.02	8" PVC	SUMP	1328.93		
328	Catch Basin	1335.83	1334.73	6" STEEL	1332.63	SUMP						
329	Catch Basin	1335.94	1334.69	6" PVC	1334.34	6" PVC	1332.34	SUMP				
331	Catch Basin	1335.06	1334.26	4" PVC	1331.36	SUMP						
333	Catch Basin	1335.64	1334.44	6" PVC	1333.69	12" CMP	1333.04	SUMP				
336	Catch Basin	1333.33	1332.38	4" PVC	1332.38	6" PVC	1330.73	Sump				
337	Catch Basin	1333.34	1332.54	4" PVC	1332.54	3" PVC	1331.09	Sump				
338	Catch Basin	1333.34	1332.79	4" PVC	1331.69	Sump						
339	Catch Basin	1331.78	1330.23	8" PVC	1330.18	6" PVC	1329.78	8" PVC	8" PVC	1329.78		
340	Catch Basin	1330.86	1329.41	8" PVC	1329.26	8" PVC	1327.86	SUMP				
346	Catch Basin	1330.41	1328.71	4" PVC	1327.46	6" PVC	1327.64	6" PVC	Sump	1326.11		
347	Catch Basin	1330.38	1329.73	4" PVC	1328.73	Sump						
348	Catch Basin	1331.09	1328.84	2" PVC PRESSUR	1327.89	6" PVC	1326.68	SUMP				
350	Catch Basin	1329.14	1327.44	6" PVC	1325.44	SUMP						
351	Catch Basin	1328.97	1327.27	6" PVC	1325.27	SUMP						
354	Catch Basin	1330.45	1329.55	6" PVC								
358	Catch Basin	1330.62	1326.27	4" PVC	1326.27	6" PVC	1326.12	6" PVC	SUMP	1324.62		
359	Catch Basin	1330.65	1327.85	4" PVC	1326.85	4" PVC	1326.55	6" PVC	6" PVC	1326.50	1324.65	SUMP
360	Catch Basin	1328.34	1326.34	6" Ductile	1324.14	SUMP						
361	Catch Basin	1330.76	1327.91	4" PVC	1326.31	6" PVC	1325.36	SUMP				
362	Catch Basin	1328.60	1326.60	6" PVC	1326.10	6" PVC	1324.60	SUMP				
363	Catch Basin	1329.63	1327.53	4" PVC	1327.28	6" PVC	1326.33	SUMP				
372	Catch Basin	1328.19	1325.09	6" PVC	1324.99	10" PVC	1323.19	SUMP				
376	Catch Basin	1326.54	1325.24	(2) 4" PVC	1324.14	6" PVC	1323.84	10" PVC	12" PVC	1322.84	1321.04	SUMP
378	Catch Basin	1326.77	1325.67	(2) 1" PVC	1325.22	6" PVC	1325.17	8" PVC				
379	Catch Basin	1328.25	1326.15	6" PVC	1326.05	6" PVC	1323.95	SUMP				
381	Catch Basin	1328.40	1327.30	6" PVC	1326.75	6" PVC	1326.65	6" PVC	SUMP	1325.10		
382	Catch Basin	1329.16	1327.46	6" PVC	1327.41	6" PVC	1324.86	SUMP				
384	Catch Basin	1330.45	1328.50	6" PVC	1328.95	6" PVC	1328.95	4" PVC	8" PVC	1328.45	1326.05	SUMP
386	Catch Basin	1331.87	1330.87	6" CONC								
390	Catch Basin	1332.09	1331.39	3" PERF	1331.29	3" PERF						
393	Catch Basin	1333.22	1332.02	4" PVC	1332.02	6" PVC	1331.72	8" PVC				
394	Catch Basin	1332.17	1330.97	6" PVC	1330.92	6" PVC						
396	Catch Basin	1333.04	1331.44	6" PVC	1328.74	Sump						
399	Catch Basin	1330.89	1329.19	6" Ductile	1326.49	Sump						
401	Catch Basin	1330.61	1328.51	6" PVC	1326.31	SUMP						
404	Catch Basin	1330.57	1328.07	10" PVC	1328.07	8" PVC	1327.87	10" PVC	SUMP	1326.37		
405	Catch Basin	1330.65	1328.70	12" PVC	1328.65	10" PVC	1328.45	8" PVC	SUMP	1326.15		
408	Catch Basin	1331.25	1328.90	8" PVC	1328.75	12" PVC	1328.05	SUMP				
411	Catch Basin	1331.24	1326.29	12" PVC	1326.24	12" PVC	1326.19	12" PVC				
412	Catch Basin	1332.36	1326.36	12" PVC	1326.26	12" PVC						
413	Catch Basin	1332.77	1326.47	12" PVC	1326.42	12" PVC						
415	Catch Basin	1334.14	1329.19	15" PVC	1327.74	SUMP						
416	Catch Basin	1334.07	1331.12	8" PVC	1329.57	SUMP						
417	Catch Basin	1344.45	1342.25	8" PVC	1339.95	SUMP						
418	Catch Basin	1334.42	1331.72	8" PVC	1329.72	8" PVC	1329.57	8" PVC	SUMP	1329.12		
419	Catch Basin	1334.42	1331.52	8" PVC	1329.82	SUMP						
421	Catch Basin	1334.60	1331.80	8" PVC	1330.10	SUMP						
422	Catch Basin	1333.07	1331.07	10" CONC	1331.02	10" CONC						
423	Catch Basin	1331.35	1329.55	6" PVC	1329.35	10" PVC	1329.25	12" CONC	SUMP	1328.55		
425	Catch Basin	1331.02	1328.97	6" PVC	1328.82	12" CONC	1328.67	12" PVC	SUMP	1327.37		
427	Catch Basin	1330.89	1328.94	6" PVC	1328.24	SUMP						
428	Catch Basin	1330.37	1328.12	8" PVC	1328.02	12" PVC	1327.87	12" PVC	SUMP	1327.52		
429	Catch Basin	1330.52	1327.72	8" N12	1327.72	12" PVC	1327.72	8" N12				
431	Catch Basin	1329.57		No Access								
432	Catch Basin	1329.74	1328.89	6" PVC								
433	Catch Basin	1329.57	1328.87	6" PVC	1328.72	6" PVC	1329.02	3" PVC				
436	Catch Basin	1332.50	1330.60	10" PVC	1330.55	10" PVC	1328.50	SUMP				
437	Catch Basin	1331.64	1330.64	10" CONC	1330.54	10" CONC	1327.64	SUMP				
439	Catch Basin	1335.00	1330.25	8" PVC	1328.50	SUMP						
441	Catch Basin	1334.96	1330.41	8" PVC	1329.36	SUMP						
442	Catch Basin	1334.85	1329.70	10" CONC	1329.70	10" CONC						
443	Catch Basin	1332.88	1330.23	10" PVC	1330.13	10" PVC	1329.08	SUMP				
444	Catch Basin	1334.58	1330.43	8" PVC	1328.78	SUMP						
446	Catch Basin	1334.05	1330.25	8" PVC	1329.05	SUMP						
447	Catch Basin	1333.69	1331.94	8" STEEL								
448	Catch Basin	1331.71	1329.96	8" STEEL	1329.86	10" PVC	1329.86	10" PVC				
449	Catch Basin	1333.40	1331.05	8" PVC	1328.90	SUMP						
451	Catch Basin	1333.18	1330.38	8" PVC	1328.58	SUMP						
452	Catch Basin	1333.08	1331.23	8" STEEL								
453	Catch Basin	1331.48	1329.68	8" PVC	1329.68	8" PVC	1328.98	SUMP				
454	Catch Basin	1331.87		Full of Debris								
455	Catch Basin	1331.25	1329.40	10" PVC								
457	Catch Basin	1329.80	1326.70	12" PVC	1326.60	18" PVC	1326.35	18" PVC				
458	Catch Basin	1330.15	1327.85	12" PVC	1325.75	SUMP						
459	Catch Basin	1329.09	1326.19	12" PVC	1325.09	18" PVC	1325.04	18" PVC				
460	Catch Basin	1328.21	1326.26	12" STEEL	1326.36	12" PVC						
461	Catch Basin	1328.75	1326.70	12" PVC								
462	Catch Basin	1328.69	1325.19	10" PVC	1324.99	18" PVC	1324.79	18" PVC				
464	Catch Basin	1328.61	1327.21	8" PVC	1328.61		1328.61					

STORM DRAIN STRUCTURES

0.4	STRUCTURE	Rim Elev	1st Invert	1st pipe size/type	2nd Invert	2nd pipe size	3rd Invert	3rd pipe size/type	4th Invert	4th pipe size
464	Catch Basin	1328.61	1327.21	8" PVC	1328.61					
466	Catch Basin	1328.55	1327.75	4" Corrugated	1326.70	6" CONC	1326.45	SUMP		
468	Catch Basin	1328.47	1327.77	3" PVC						
469	Catch Basin	1329.24	1326.69	12" PVC	1326.64	12" PVC	1325.24	SUMP		
470	Catch Basin	1329.52	1326.92	8" PVC	1326.82	(3) 12" PVC	1325.72	SUMP		
471	Catch Basin	1329.30	1327.40	6" PVC	1325.80	SUMP				
472	Catch Basin	1329.74	1327.59	6" PVC	1326.24	SUMP				
473	Catch Basin	1329.98	1326.88	12" PVC	1326.83	12" PVC	1326.18	SUMP		
474	Catch Basin	1330.62	1329.52	6" STEEL						
475	Catch Basin	1330.88	1327.98	12" PVC	1327.93	12" PVC	1326.58	SUMP		
476	Catch Basin	1331.55	1327.20	12" PVC	1325.55	SUMP				
477	Catch Basin	1330.68	1329.68	4" PVC	1329.08	10" PVC	1329.08	10" PVC		
478	Catch Basin	1332.27	1330.50	8" STEEL						
479	Catch Basin	1332.98	1331.28	6" STEEL						
482	Catch Basin	1327.29	1325.64	4" Corrugated	1325.44	6" PVC	1323.99	SUMP		
483	Catch Basin	1327.87	1326.00	6" PVC	1325.52	12" PVC	1324.37	SUMP		
484	Catch Basin	1326.93	1325.28	12" PVC	1325.23	12" PVC	1323.43	SUMP		
485	Catch Basin	1327.22	1325.32	6" PVC	1323.72	SUMP				
486	Catch Basin	1327.14	1324.79	12" PVC	1324.79	8" PVC	1323.64	SUMP		
487	Catch Basin	1327.30	1324.60	6" PVC	1324.50	12" PVC	1323.80	SUMP		
488	Catch Basin	1326.34	1325.24	6" PVC	1322.64	1" PVC	1322.04	SUMP		
489	Catch Basin	1326.62	1325.47	2" PVC	1324.57	12" PVC	1324.52	8" PVC	12" PVC	1324.52
490	Catch Basin	1326.00	1324.00	10" CONC	1323.85	8" CONC				
492	Catch Basin	1326.81	1325.06	6" PVC	1323.11	SUMP				
495	Catch Basin	1327.02	1325.27	8" PVC	1323.32	SUMP				
496	Catch Basin	1326.47	1324.72	8" PVC	1322.77	SUMP				
497	Catch Basin	1326.44	1324.69	8" PVC	1322.74	8" PVC				
499	Catch Basin	1325.12	1321.82	8" PVC	1320.02	SUMP				
500	Catch Basin	1324.55	1320.75	18" PVC	1320.00	12" PVC	1318.65	24" PVC		
501	Catch Basin	1324.96	1322.36	8" PVC	1321.31	18" PVC	1321.26	18" PVC		
502	Catch Basin	1324.91	1321.71	8" PVC	1321.51	18" PVC	1321.41	18" PVC		
503	Catch Basin	1325.10	1321.70	18" PVC	1321.65	18" PVC				
504	Catch Basin	1325.37	1322.47	8" PVC	1322.37	18" PVC	1322.27	18" PVC		
505	Catch Basin	1327.75	1322.45	12" PVC	1322.25	12" PVC				
507	Catch Basin	1327.05	1324.50	8" PVC	1324.60	8" PVC	1322.85	SUMP		
509	Catch Basin	1327.79	1324.69	10" PVC	1324.54	18" PVC	1324.54	18" PVC		
511	Catch Basin	1324.10	1322.55	8" PVC	1322.55	8" PVC				
512	Catch Basin	1324.27	1315.07	24" PVC	1314.22	12" PVC	1314.47	38" PVC		
512	Catch Basin	1324.30	1322.65	8" PVC	1322.45	8" PVC	1322.30	SUMP		
513	Catch Basin	1324.85	1323.25	8" PVC	1320.45	SUMP				
516	Catch Basin	1323.68	1322.88	6" PVC						
519	Catch Basin	1324.47	1322.77	8" PVC	1322.67	8" PVC	1321.72	Sump		
522	Catch Basin	1325.18	1324.28	6" PVC	1323.58	SUMP				
526	Catch Basin	1324.81	1323.26	8" PVC	1320.81	SUMP				
529	Catch Basin	1326.89	1325.09	6" PVC	1323.19	SUMP				
531	Catch Basin	1327.19	1324.69	8" PVC	1322.79	SUMP				
534	Catch Basin	1326.84	1323.89	12" PVC	1323.84	12" PVC	1323.14	SUMP		
536	Catch Basin	1327.75	1324.35	8" PVC	1323.45	SUMP				
539	Catch Basin	1328.04	1331.54	6" PVC	1324.54	8" PVC	1324.54	8" PVC	Sump	1323.54
541	Catch Basin	1327.55	1325.55	6" PVC	1325.50	8" PVC	1324.00	Sump		
543	Catch Basin	1328.72	1326.27	6" PVC	1326.02	SUMP				
545	Catch Basin	1327.85	1327.25	WATER LEVEL	1326.85	SUMP				
546	Catch Basin	1325.40	1324.50	6" PVC	1323.80	SUMP				
547	Catch Basin	1326.51		No Access						
548	Catch Basin	1324.61		No Access						
549	Catch Basin	1324.90		No Access						
550	Catch Basin	1324.90	1323.50	8" PVC						
551	Catch Basin	1324.28	1314.63	36" PVC	1314.58	36" Sanitite				
552	Catch Basin	1324.35	1323.35	6" PVC Oil Sep.						
553	Catch Basin	1324.29	1322.04	8" PVC	1319.99	SUMP				
556	Catch Basin	1329.32	1326.52	6" PVC	1325.82	8" PVC	1325.72	10" PVC		
557	Catch Basin	1329.16		Full of Debris						
558	Catch Basin	1328.73	1326.43	6" PVC	1326.23	6" PVC	1325.23	Sump		
559	Catch Basin	1329.45	1326.85	6" PVC	1326.80	6" PVC				
561	Catch Basin	1329.49	1328.59	6" PVC						
562	Catch Basin	1325.83	1325.83							
563	Catch Basin	1328.22	1327.32	6" PVC						
568	Catch Basin	1325.50		BOLTED SHUT						
580	Catch Basin	1326.55	1325.95	3" PVC						
584	Catch Basin	1329.52	1328.52	SUMP-NO PIPES						
591	Catch Basin	1333.55	1331.80	12" CMP	1331.85	8" PVC	1331.75	12" CMP		
596	Catch Basin	1331.77	1330.37	8" PVC	1327.67	SUMP				
597	Catch Basin	1331.78	1329.88	8" PVC	1327.68	SUMP				
599	Catch Basin	1331.08	1330.18	6" PVC						
600	Catch Basin	1330.96	1329.61	12" PVC	1328.96	12" PVC	1326.81	SUMP		
602	Catch Basin	1330.90	1329.60	6" PVC						
604	Catch Basin	1330.91	1329.61	6" PVC						
605	Catch Basin	1331.06	1330.16	6" PVC						
606	Catch Basin	1330.82	1329.92	6" PVC						
607	Catch Basin	1331.08	1330.18	6" PVC						
609	Catch Basin	1331.07	1330.17	6" PVC						
610	Catch Basin	1331.12	1330.22	6" PVC						
613	Catch Basin	1326.87	1325.97	6" PVC						
614	Catch Basin	1329.75	1327.60	6" PVC	1325.45	SUMP				
614	Catch Basin	1330.36	1329.21	6" PVC						
615	Catch Basin	1330.36	1327.96	SUMP-NO PIPES						
616	Catch Basin	1328.84	1326.99	8" PVC	1324.54	SUMP				
617	Catch Basin	1328.74	1327.99	4" PVC	1327.09	SUMP				
618	Catch Basin	1329.14	1328.39	4" PVC	1327.48	SUMP				
620	Catch Basin	1329.02	1328.27	4" PVC	1327.37	SUMP				
621	Catch Basin	1328.36	1327.61	4" PVC	1326.71	SUMP				
622	Catch Basin	1328.59	1327.84	4" PVC	1326.94	SUMP				
623	Catch Basin	1328.56	1327.81	4" PVC	1326.91	SUMP				
624	Catch Basin	1328.65	1330.45	12" PVC	1325.30	18" C900	1324.35	Sump		
629	Catch Basin	1330.48	1329.12	2" PVC Pressure	1328.88	6" STEEL	1328.53	(2) 10" PVC	SUMP	1327.08
633	Catch Basin	1328.49	1325.39	6" PVC						
636	Catch Basin	1326.60	1325.95	2" PVC	1325.25	8" PVC				