



FORT LEAVENWORTH
DPW

MARK	DESCRIPTION	DATE

DESIGNED BY: DPL	ISSUE DATE: 07/31/2024	
	PROJECT NO.:	
	DRAWN BY: DPL	
	CHECKED BY: DPL	
DIRECTORATE OF PUBLIC WORKS ENGINEERING DIVISION DESIGN BRANCH		820 MCLELLAN AVE, FORT LEAVENWORTH, KS 66027-1292
SIZE:		

GRANT AVENUE STRIPING PLAN

SHEET ID

C2

SHEET KEYNOTES

- 1

STOP BAR
- 2

TYPE I CROSSWALK
- 3

TYPE II CROSSWALK
- 4

4" SOLID WHITE
- 5

4" DOUBLE YELLOW
- 6

4" DASHED WHITE

7

12" SOLID WHITE

8

ONLY

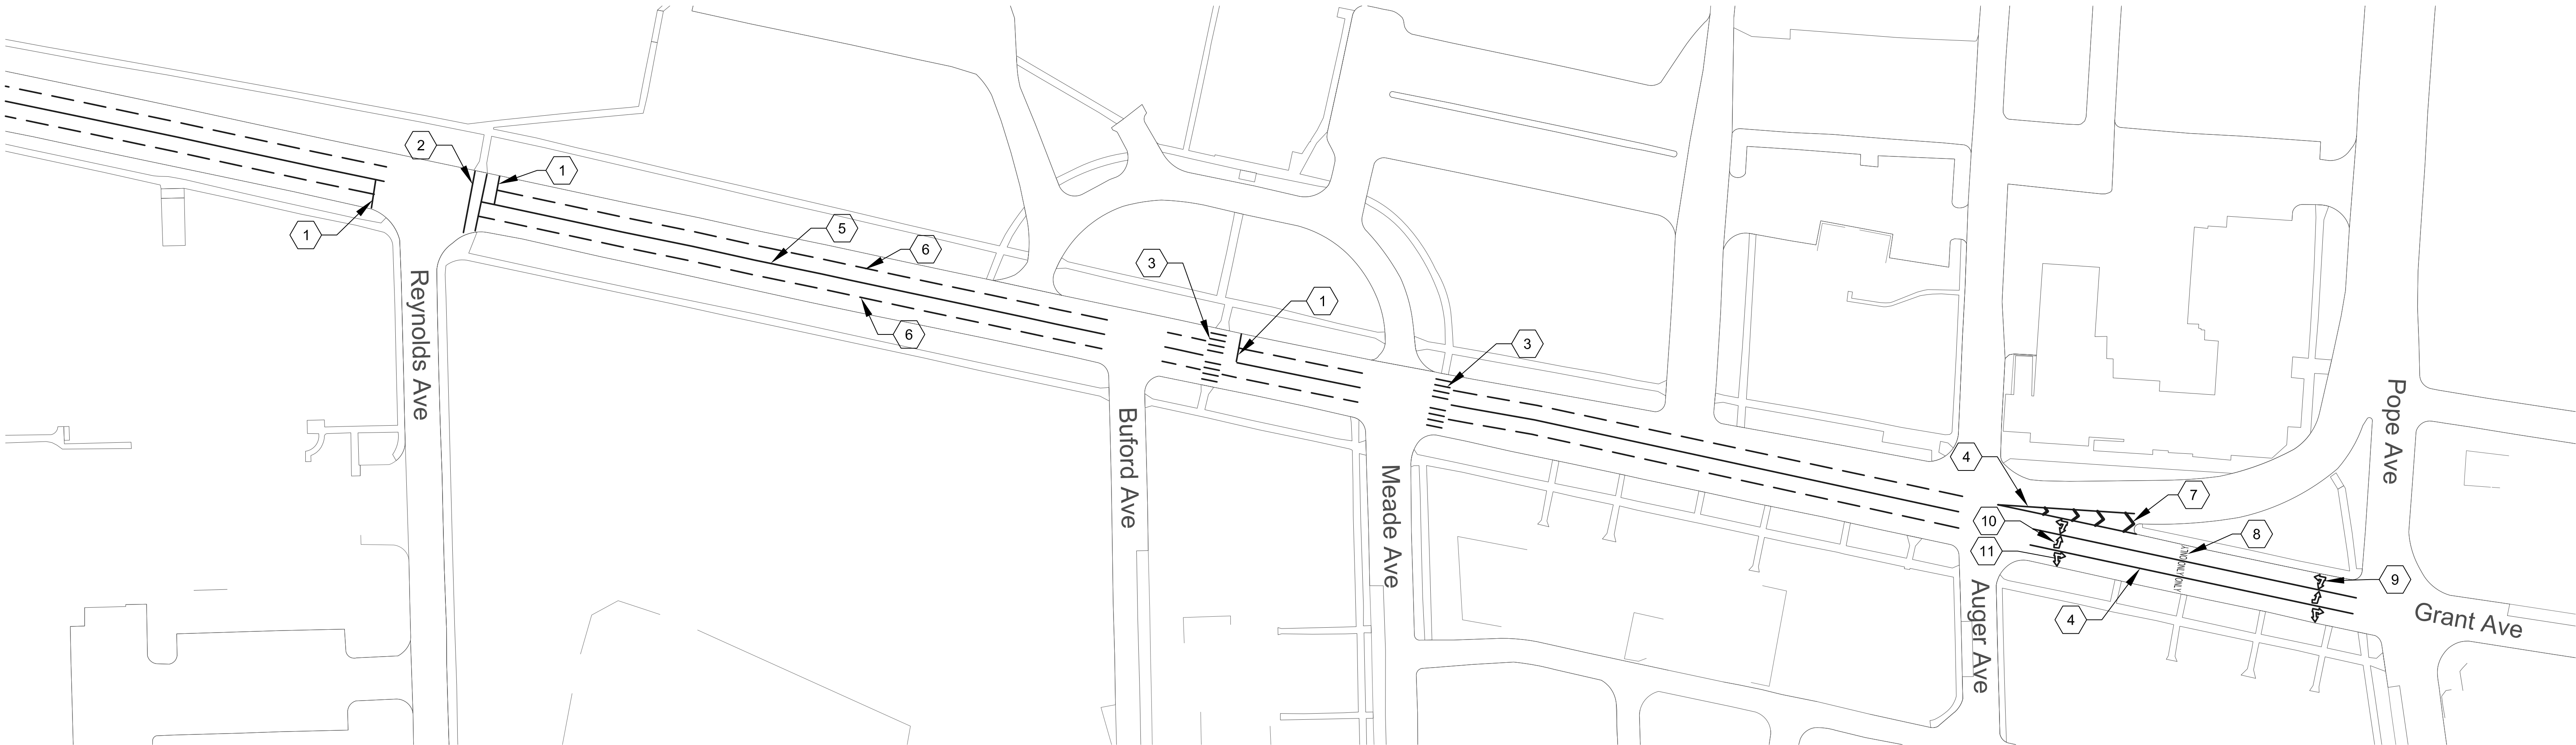
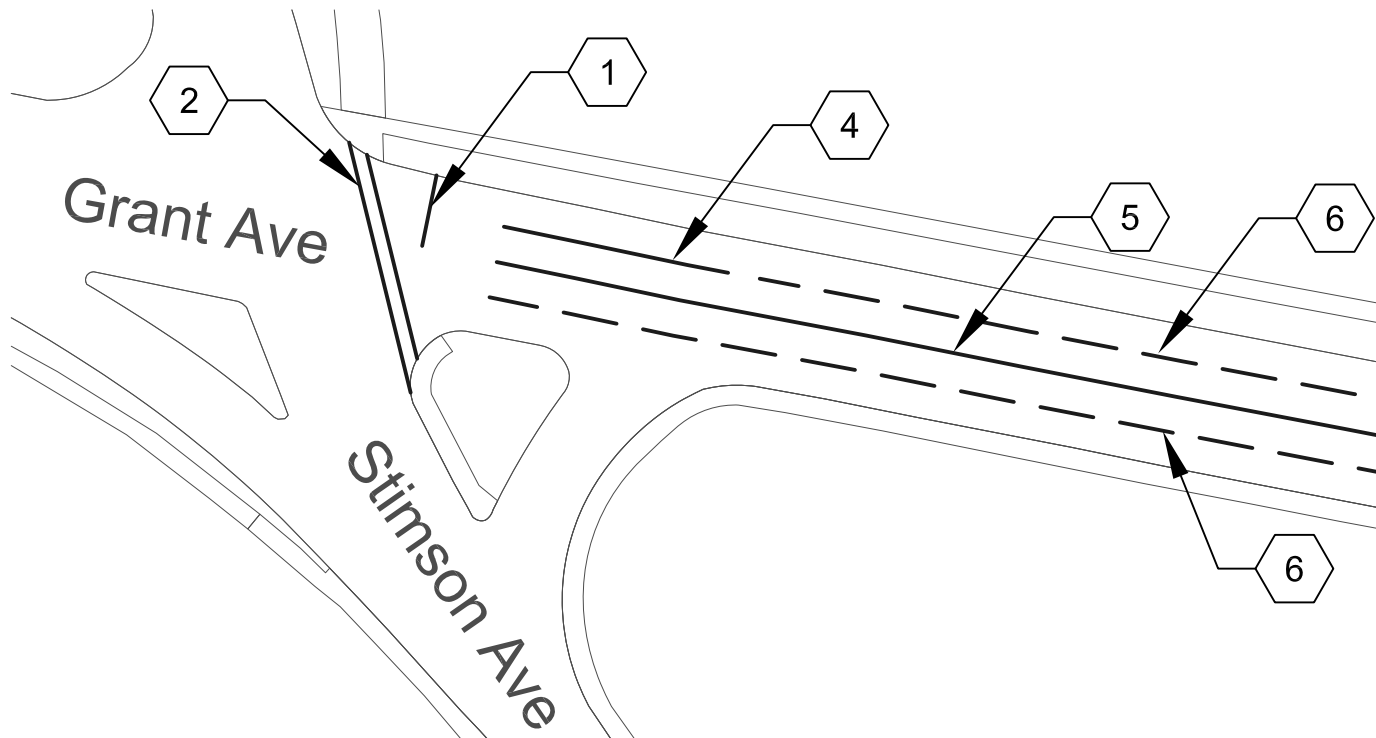
9

STRAIGHT LEFT TURN ARROW

10

LEFT TURN ARROW

11

STRAIGHT RIGHT TURN ARROW

1

C2

GRANT AVENUE - STRIPING
SCALE: 1" = 60'

