


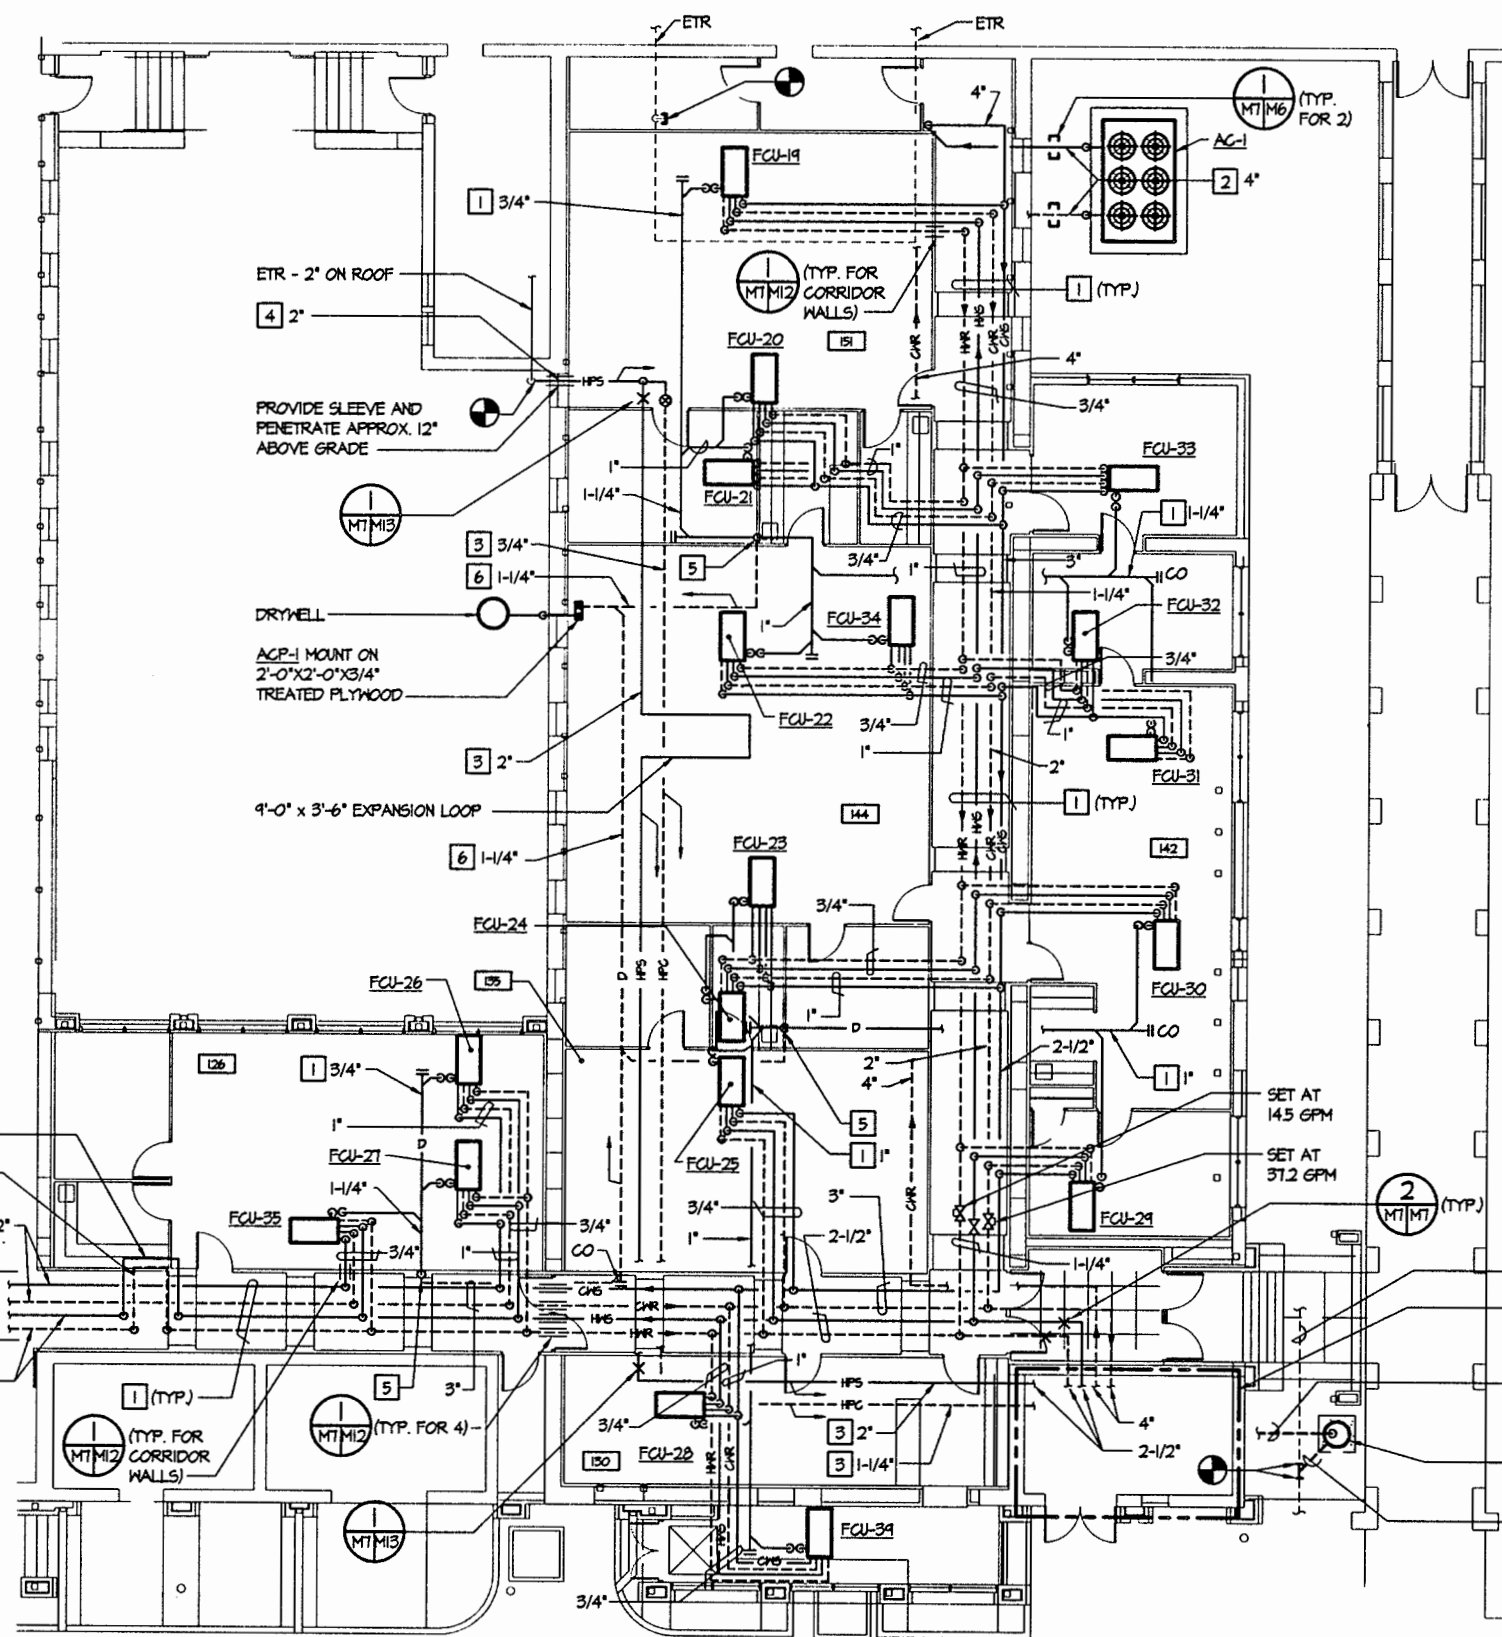


NEW WORK NOTES THIS SHEET

- 1 PROVIDE PIPING, INSULATION, HANGERS AND SUPPORTS. RUN IN CEILING. SIZE AS INDICATED.
- 2 PROVIDE PIPING, INSULATION, SUPPORTS, HEAT TAPE, HANGERS AND METAL JACKET. SIZE AS INDICATED.
- 3 PROVIDE PIPING, INSULATION, SUPPORTS AND HANGERS. RUN IN CRAWLSPACE. SIZE AS INDICATED.
- 4 PROVIDE PIPING, INSULATION, SUPPORTS, HANGERS AND METAL JACKET. SIZE AS INDICATED.
- 5 1-1/4\" PIPE, TURN DOWN IN WALL PARTITION AND RUN IN CRAWL SPACE AS INDICATED.
- 6 PROVIDE PIPING, INSULATION, HANGERS AND SUPPORTS. RUN IN CRAWL SPACE. SIZE AS INDICATED.

ROOM SCHEDULE

124	OFFICE
125	WORK ROOM
126	OPEN OFFICE
127	ELECTRICAL ROOM
128	ELECTRICAL ROOM
129	ELECTRICAL ROOM
130	ADMINISTRATION
131	MAIL
132	MECHANICAL ROOM
133	VESTIBULE
134	CORRIDOR
135	OPEN OFFICE
136	OFFICE
137	WORK ROOM
138	OFFICE
139	OFFICE
140	CLOSET
141	OFFICE
142	OPEN OFFICE
143	CORRIDOR
144	OPEN OFFICE
145	CLOSET
146	OFFICE
147	CONFERENCE
148	WORK ROOM
149	WORK ROOM
150	OFFICE
151	OPEN OFFICE
152	VESTIBULE
153	ADP CLOSET
154	VENDING

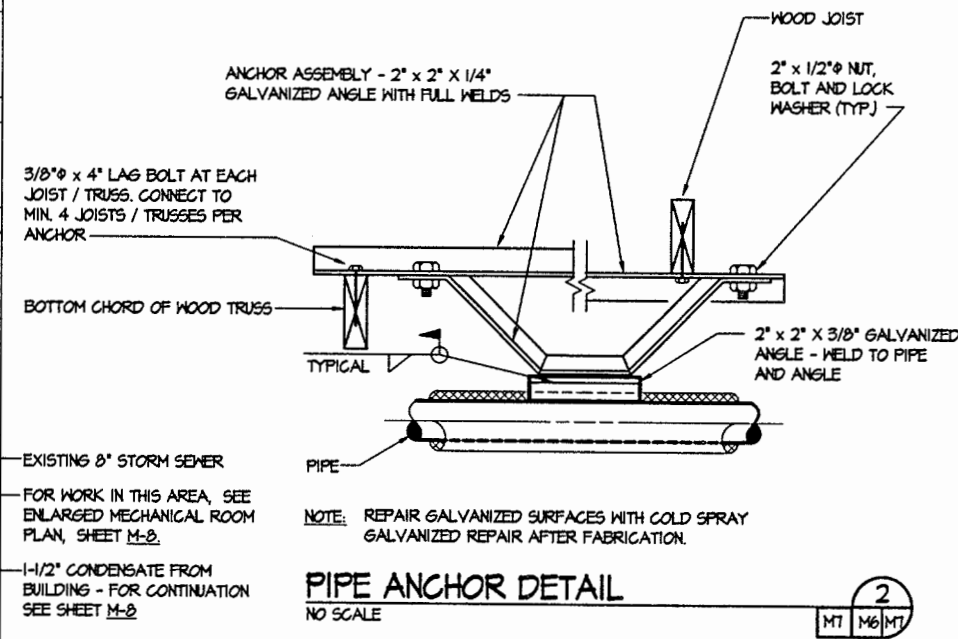


HVAC PARTIAL NEW WORK PLAN - PIPING - EAST

SCALE: 1/8\"=1'-0\"

NOTE: RUNOUTS ARE 3/4\" UNLESS NOTED OTHERWISE.

GRAPHIC SCALES

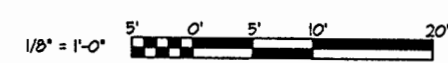

HUDSON + ASSOCS, ARCHITECTS
503 BOTETOURT STREET
NORFOLK, VA 23510

JOB ORDER NO. 1323093
DES. NKC DR. WSH CHK. PDP
DR. MGR. J.H. GALLEY, JR.
SUBMITTED BY: DATE:

EX. J. STARK
DR. DR. R.H. IVES, JR.

APPROVED: DATE: 10/14/94
DR. CAPT DJ FELTES (SCUN)
APPROVED: DATE: 10/26/94
FOR C.O. FOR COMMAND OFFICER, NAVFAC

DEPARTMENT OF THE NAVY
NAVAL FACILITIES ENGINEERING COMMAND
NAVY PUBLIC WORKS CENTER
NAVAL STATION
CONJUNCT AREA
NORFOLK, VA

ADDITIONS & RENOVATIONS
TO BUILDINGS NH-15, NH-16, & NH-17

HVAC PARTIAL NEW WORK PLAN-PIPE

DR. CODE IDENT NO. NAVFAC DRAWING NO. PWC DRAWING NO.
D 80091 4,287,831 15060BB
CONSTR. CONTR. NO. N62470-94-B-2232
SCALE: GRAPHIC SPEC 05-94-2232 SHEET 55 OF 78

