



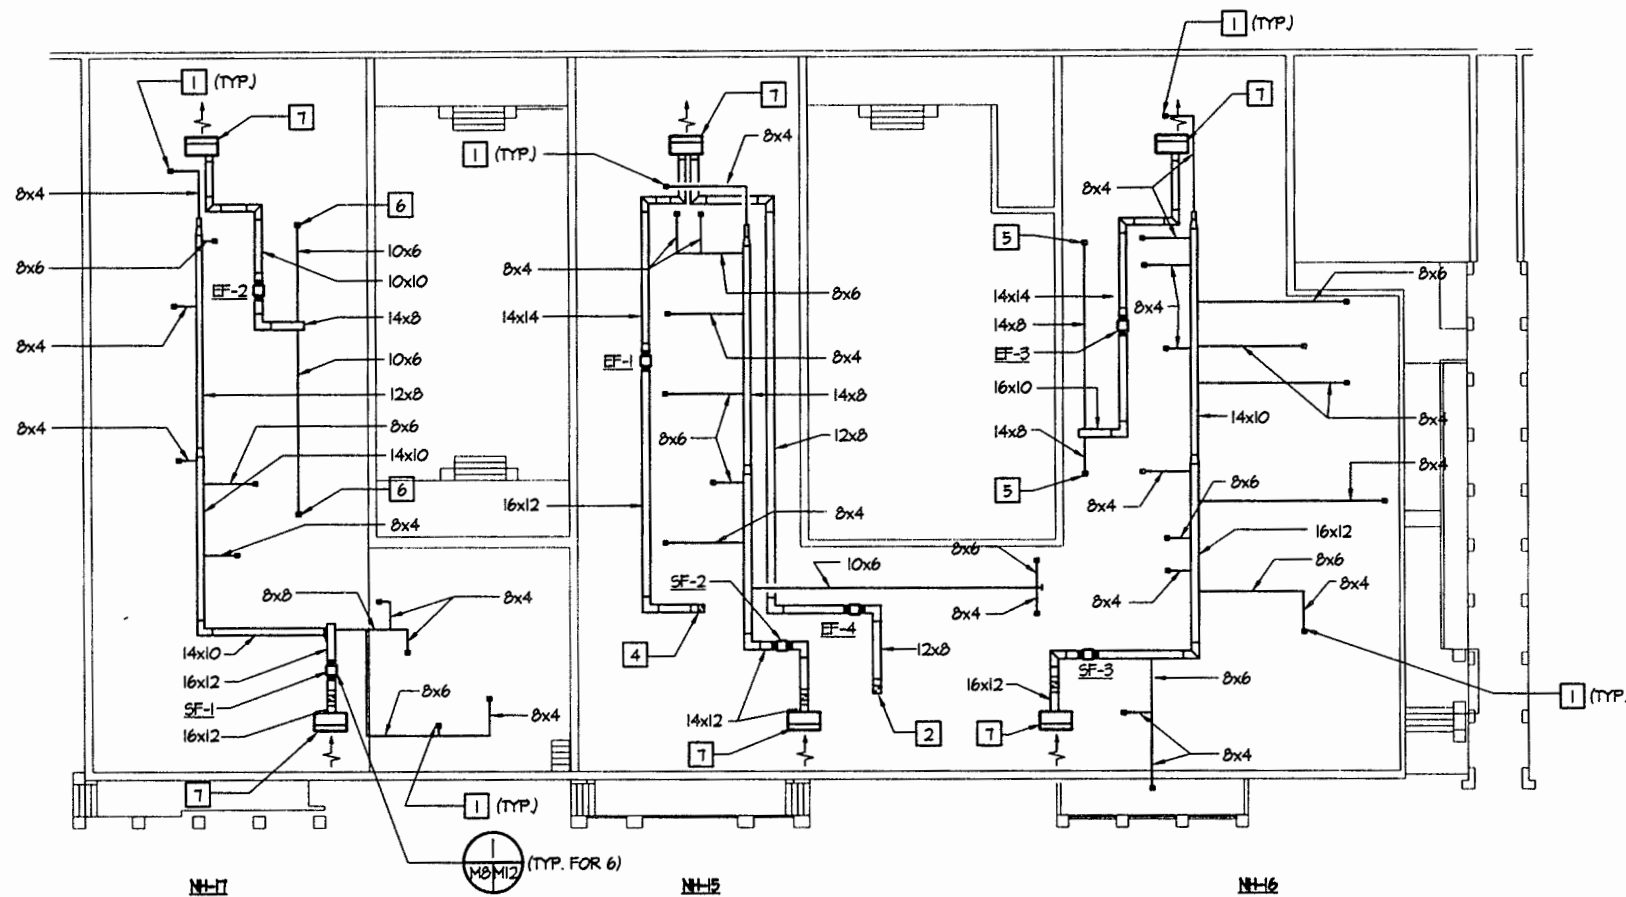

- NOTE: 1. SINGLE LINE DUCTWORK SHOWN FOR CLARITY FOR SMALLER DUCT SIZES.
2. ALL DUCTWORK ON THIS PLAN RUN IN ATTIC ABOVE BOTTOM CHORD OF TRUSSES UNLESS OTHERWISE NOTED.


HVAC ATTIC PLAN

SCALE: 1/16"=1'-0"

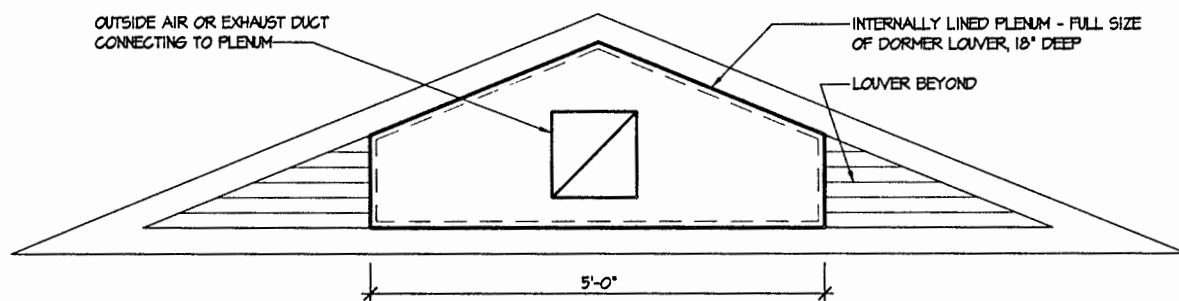


PLENUM AT DORMER LOUVER DETAIL
NO SCALE

STEEL ANGLE OR CHANNEL - MINIMUM
2" x 2" x 1/4", SPAN MINIMUM OF THREE
TRUSSES (TYPICAL FOR 2 PER FAN
COIL UNIT)

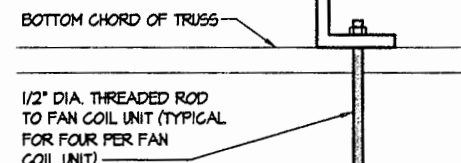

FCU SUPPORT DETAIL
NO SCALE

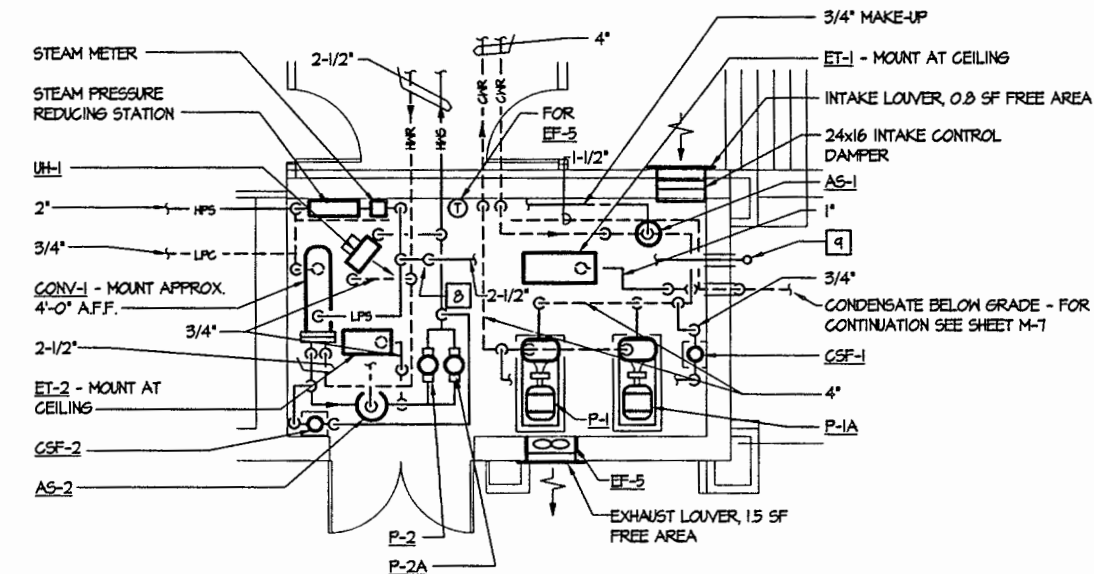

NOTE: SEE FLOW DIAGRAMS, SHEET M-10.


ENLARGED MECHANICAL ROOM PLAN

SCALE: 1/4"=1'-0"

NEW WORK NOTES THIS SHEET

- OUTSIDE AIR DUCTWORK DOWN TO FAN COIL UNIT MOUNTED ABOVE CEILING. PROVIDE VOLUME DAMPER IN RISER.
- 12" x 8" EXHAUST AIR DUCTWORK DOWN. FOR CONTINUATION SEE SHEET M-5.
- NOT USED
- 16" x 12" EXHAUST AIR DUCTWORK DOWN TO ABOVE CEILING. SEE SHEET M-4 FOR CONTINUATION.
- 14" x 8" EXHAUST AIR DUCTWORK DOWN TO REGISTER IN CEILING. PROVIDE VOLUME DAMPER IN RISER. SEE SHEETS M-4 & M-5 FOR CONTINUATION.
- 10" x 6" EXHAUST AIR DUCTWORK DOWN TO REGISTER IN CEILING. PROVIDE VOLUME DAMPER IN RISER. SEE SHEETS M-4 & M-5 FOR CONTINUATION.
- CONNECT TO DORMER LOUVER WITH 18" DEEP PLENUM. PROVIDE FASTENERS AND GASKETS. SEE DETAIL THIS SHEET.
- DRIP PAN ELBOW - DISCHARGE TO EXTERIOR OF BUILDING.
- TERMINATE DRIP PAN ELBOW DISCHARGE WITH ELBOW AND PIPE AT MINIMUM 10'-0" ABOVE GRADE.

GRAPHIC SCALES

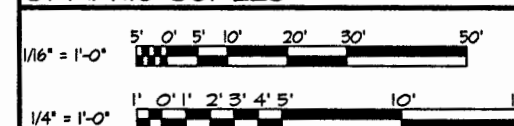

HUDSON + ASSOCS, ARCHITECTS
503 BOTETOURT STREET
NORFOLK, VA 23510

JOB ORDER NO. 1323093
DES. NKC | DR. WSH | CHK. PDP
BR. MGR. J. H. GALLEY, JR.
SUBMITTED BY: DATE:

DEPARTMENT OF THE NAVY
NAVAL FACILITIES ENGINEERING COMMAND
NAVY PUBLIC WORKS CENTER
NAVAL STATION
CONCRETE AREA
NORFOLK, VA

ADDITIONS & RENOVATIONS
TO BUILDINGS NH-15, NH-16, & NH-17

HVAC ATTIC PLAN & ENLARGED PLAN

EXC. J. STARK
DR. DR. R.H. IVES, JR.
APPROVED: DATE: 10/14/94
DR. CAPT. DJ FELTES (SCUGN)
APPROVED: DATE: 10/14/94
FOR C.O. FOR COMMAND OFFICER, NAVFAC

DR. CODE IDENT NO. NAVFAC DRAWING NO. PWC DRAWING NO.
D 80091 4,287,832 15060CB
CONSTR. CONTR. NO. N62470-94-B-2232
SCALE: GRAPHIC SPEC 05-94-2232 SHEET 56 OF 78

M-8